

# (仮称)sumitsuboストア 新築工事

## 建 築 図

設計: ainote建築株式会社


### 建築概要

|       |                                 |
|-------|---------------------------------|
| 用 途   | 物販店舗(食品スーパー)                    |
| 構造・階数 | 鉄骨造 地上1階                        |
| 建築面積  | 219.01 m <sup>2</sup> (延床面積 同じ) |
| 最高高さ  | GL+5,500(パラペット天端)               |
| 屋 根   | ガルバリウム鋼板 折板葺き                   |
| 外 壁   | ALCパネル t=100 縦張り 吹付塗装           |
| 外部建具  | アルミ製ほか(A-04 建具表による)             |

### 図面リスト


|      |           |       |
|------|-----------|-------|
| A-01 | 表紙・図面リスト  | -     |
| A-02 | 1階平面図     | 1/100 |
| A-03 | 立面図(東西南北) | 1/100 |
| A-04 | 建具表       | -     |

|                              |                   |            |      |
|------------------------------|-------------------|------------|------|
| 物件名<br>(仮称)sumitsuboストア 新築工事 | 図面名<br>表紙・図面リスト   | 縮 尺<br>-   | 図面番号 |
| 設 計<br>ainote建築株式会社          | 日 付<br>2026-08-25 | 頁<br>1 / 4 | A-01 |

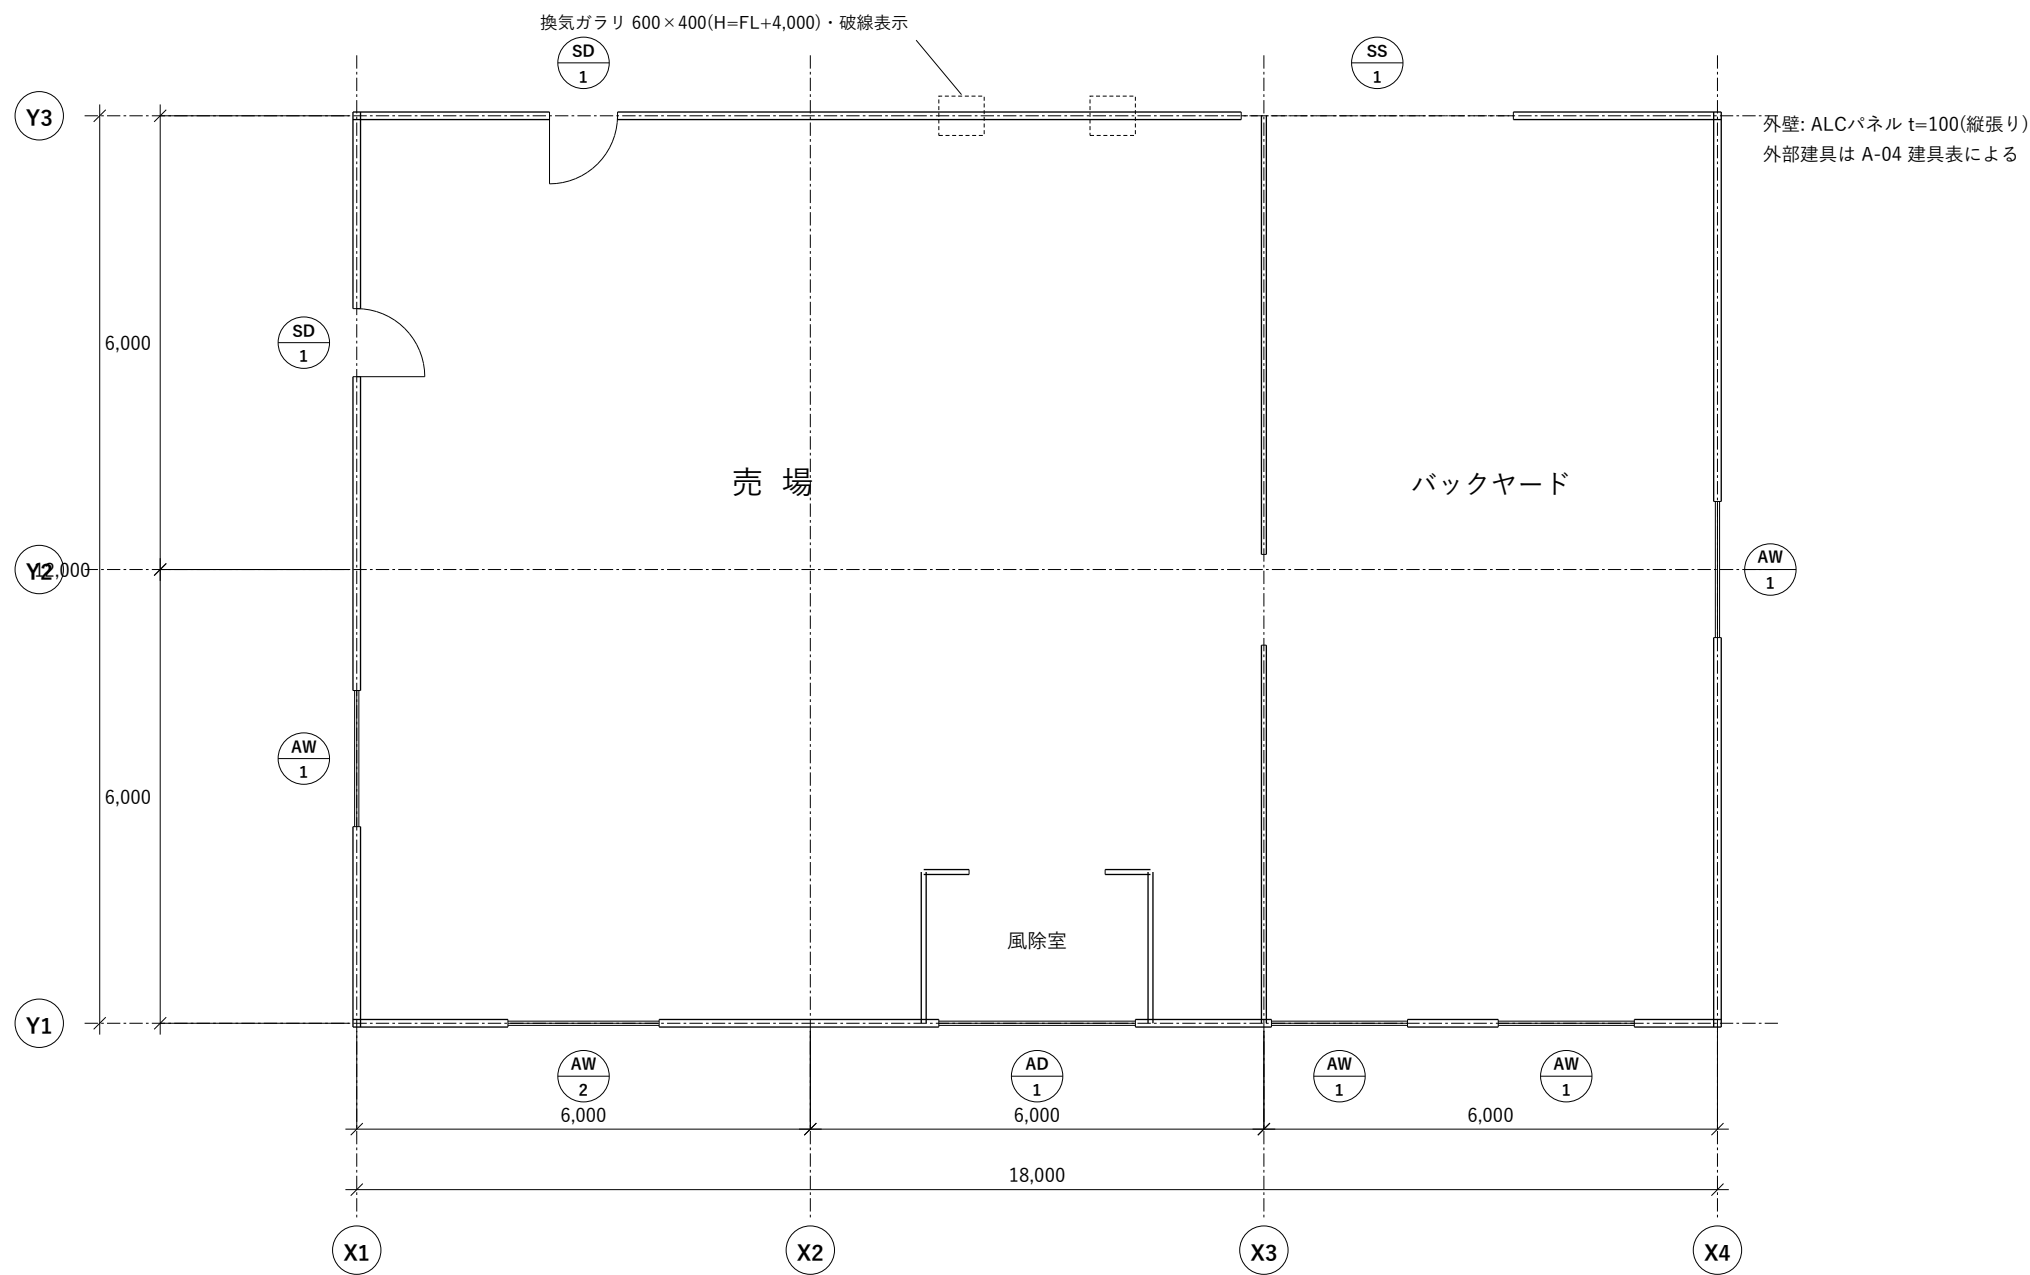


1階平面図 S=1/100


|                              |                   |              |      |
|------------------------------|-------------------|--------------|------|
| 物件名<br>(仮称)sumitsuboストア 新築工事 | 図面名<br>1階平面図      | 縮 尺<br>1/100 | 図面番号 |
| 設 計<br>ainote建築株式会社          | 日 付<br>2026-08-25 | 頁<br>2 / 4   | A-02 |

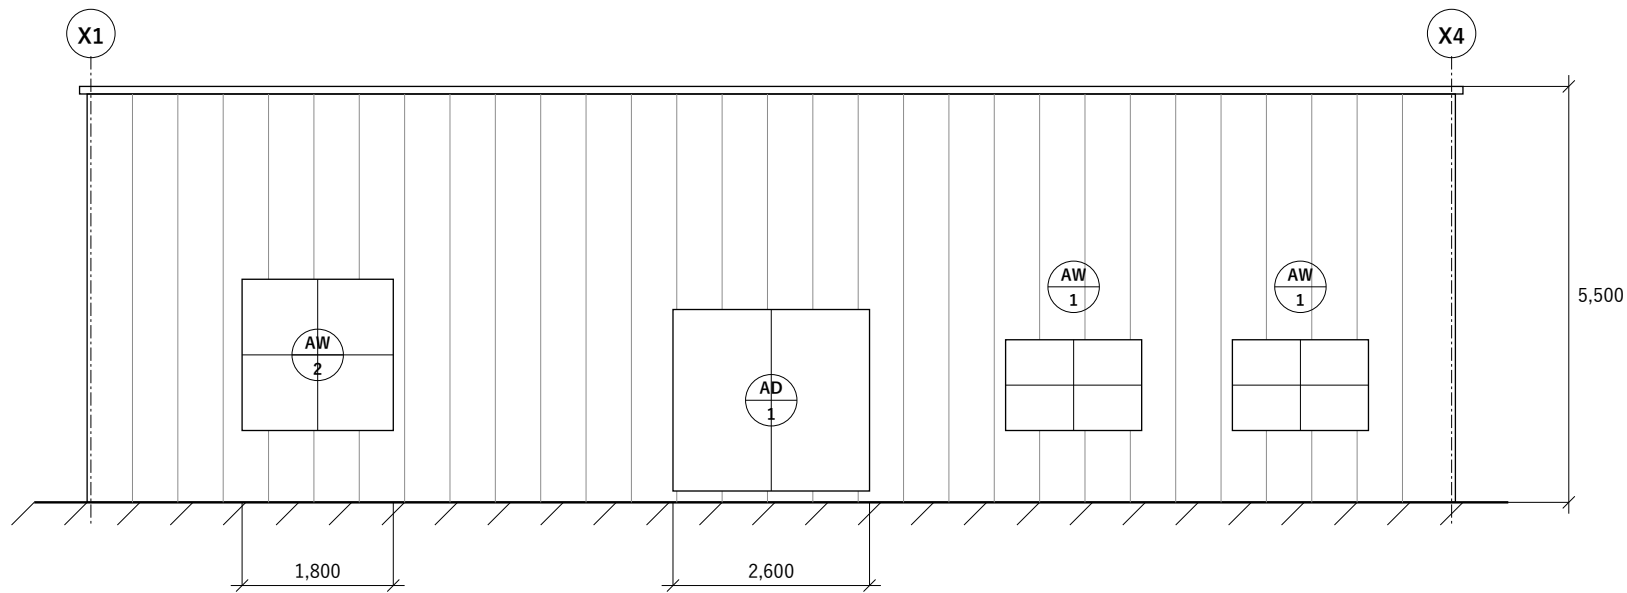


南立面図 S=1/100

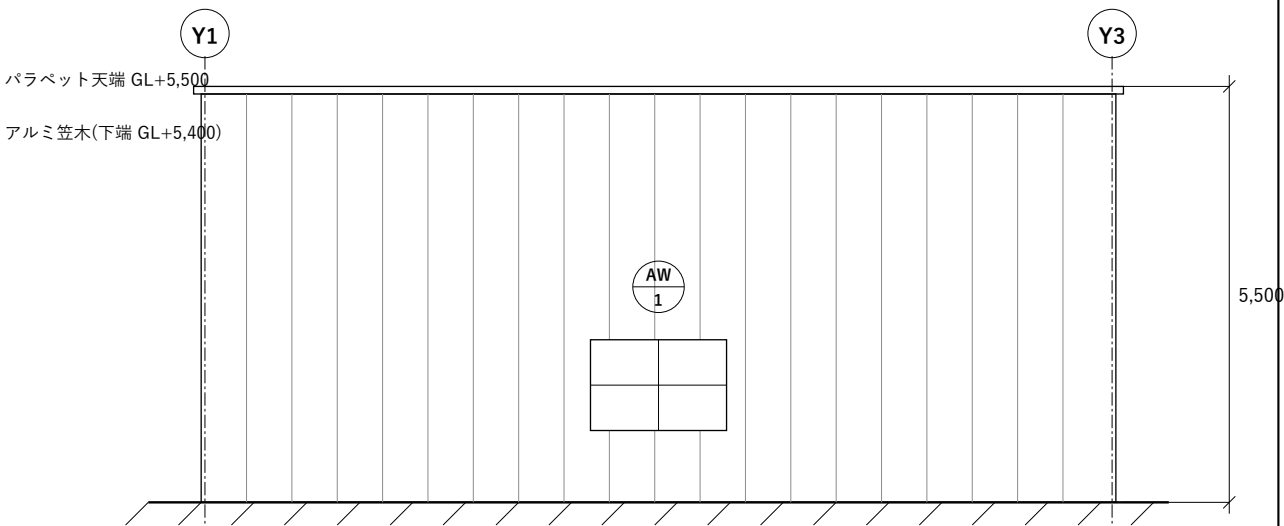

東立面図 S=1/100

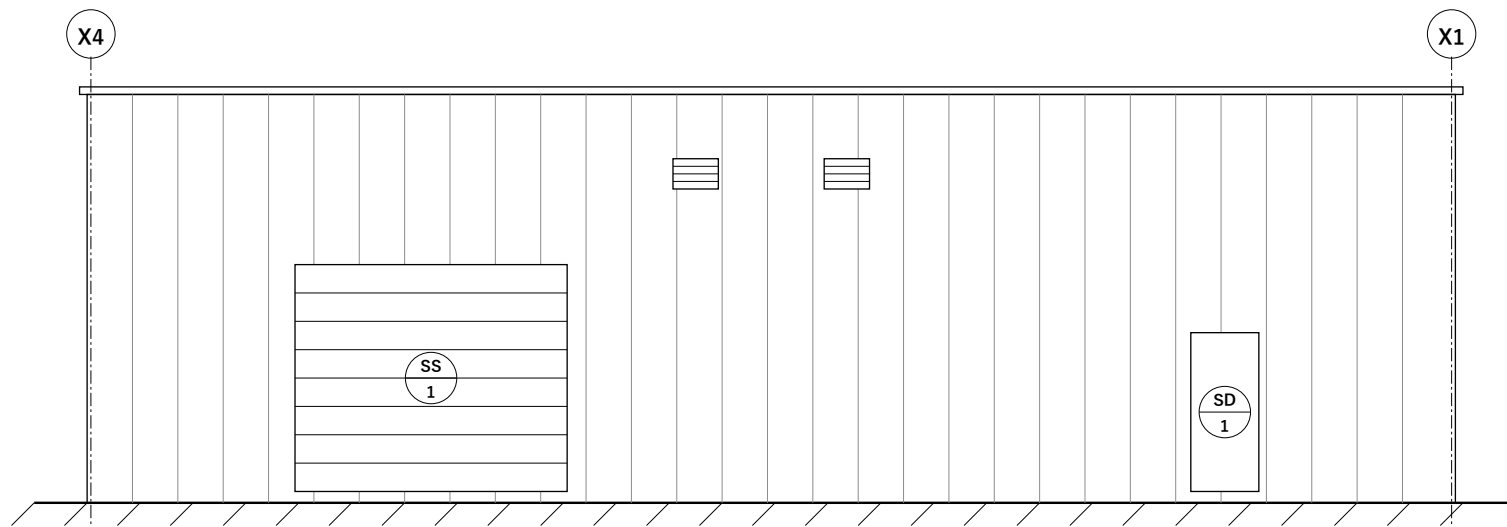






北立面図 S=1/100

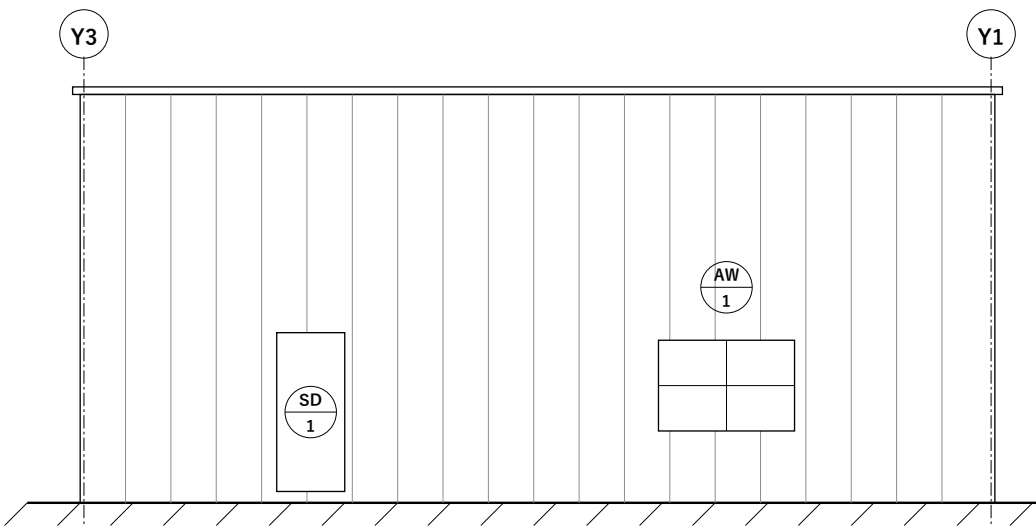

西立面図 S=1/100

|                              |                  |             |      |
|------------------------------|------------------|-------------|------|
| 物件名<br>(仮称)sumitsuboストア 新築工事 | 図面名<br>立面図(東西南北) | 縮尺<br>1/100 | 図面番号 |
| 設計<br>ainote建築株式会社           | 日付<br>2026-08-25 | 頁<br>3 / 4  | A-03 |

建 具 表(外部建具)
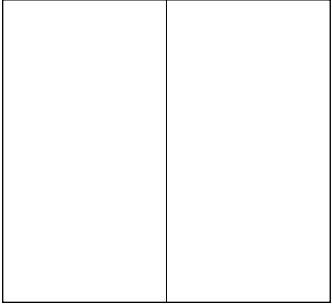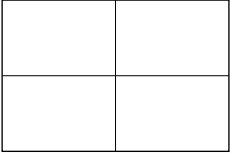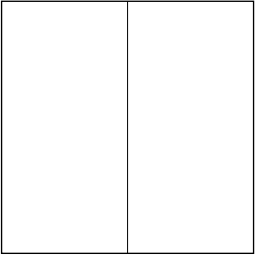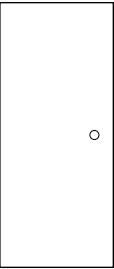 
| 符号     | <div>AD<br/>1</div>                                                                                                | <div>AW<br/>1</div>                                                                                             | <div>AW<br/>2</div>                                                                                              | <div>SD<br/>1</div>                                                                                             | <div>SS<br/>1</div>                                                                                                |
|--------|---|---|---|---|---|
| 姿図     | <div><div>(自動ドア(引分け))</div></div> | <div><div>(引違い窓)</div></div> | <div><div>(はめ殺し窓)</div></div> | <div><div>(片開き扉)</div></div> | <div><div>(軽量シャッター)</div></div> |
| 寸法 W×H | 2,600 × 2,400   | 1,800 × 1,200                                                                                                   | 2,000 × 2,000   | 900 × 2,100   | 3,600 × 3,000   |
| 数量     | 1 箇所   | 4 箇所   | 1 箇所   | 2 箇所   | 1 箇所   |
| 材質・仕上  | アルミ製   | アルミ製   | アルミ製   | 鋼製フラッシュ   | スチール製・電動   |
| ガラス    | 強化ガラス t=10   | 複層ガラス   | 複層ガラス   | -   | -   |
| 備考     | 正面入口・風除室   | 網戸付   | -   | 錠前付   | 搬入口   |

注1) 寸法は内法基準の呼称寸法とする。取合いの詳細は施工図による。

注2) 本表は外部建具を示す。

|                              |                   |            |      |
|------------------------------|-------------------|------------|------|
| 物件名<br>(仮称)sumitsuboストア 新築工事 | 図面名<br>建具表        | 縮 尺<br>-   | 図面番号 |
| 設 計<br>ainote建築株式会社          | 日 付<br>2026-08-25 | 頁<br>4 / 4 | A-04 |