

# (仮称)ハルカゼストア 白鷺緑丘店 新築工事

## 建 築 図

|       |                                                    |
|-------|----------------------------------------------------|
| 建 築 主 | 株式会社ハルカゼストア （ハルカゼストア 様）                            |
| 所 在 地 | 碧海県白鷺市栄町二丁目5番1号                                    |
| 設 計 者 | あおば建築設計事務所 一級建築士事務所 碧海県知事 登録第00013号                |
| 所 在 地 | 碧海県白鷺市中央三丁目1番8号 電話番号 03-0000-0000 FAX 03-0000-0001 |
| 管理建築士 | 白石 康晴                                              |
| 担 当 者 | 早川 真澄                                              |
| 建築場所  | 碧海県白鷺市緑丘三丁目14番1号                                   |
| 作 成 日 | 2026 年 9 月 18 日                                    |

### 図 面 リ ス ト

| 図面番号 | 図 面 名     | 縮尺(A1)  | 縮尺(A3)  | 備 考        |
|------|-----------|---------|---------|------------|
| A-00 | 図面目録      | -       | -       |            |
| A-01 | 設計概要・案内図  | 1/2,500 | 1/2,500 | 案内図を含む     |
| A-02 | 配置図       | 1/200   | 1/200   |            |
| A-03 | 特記仕様書     | -       | -       | 共通仕様は本書による |
| A-04 | 外部仕上表     | -       | -       |            |
| A-05 | 1階平面図     | 1/50    | 1/100   |            |
| A-06 | 屋根伏図      | 1/50    | 1/100   |            |
| A-07 | 立面図(東西南北) | 1/50    | 1/100   |            |
| A-08 | 断面図       | 1/50    | 1/100   |            |
| A-09 | 建具キープラン   | 1/50    | 1/100   | 建具符号の位置    |
| A-10 | 建具表       | 1/30    | 1/60    | 外部建具       |

【 注 意 】

この図面は架空の物件です。実在の物件・団体・人物とは関係ありません。

PDFマスクツールの動きを見せるためのサンプルです。

|                                  |   |  |                                                                                       |                                                                                       |                                                                                       |                      |                                           |                               |                      |     |  |
|----------------------------------|---|--|---------------------------------------------------------------------------------------|---------------------------------------------------------------------------------------|---------------------------------------------------------------------------------------|----------------------|-------------------------------------------|-------------------------------|----------------------|-----|--|
| ・変更略歴<br>.....<br>.....<br>..... | <div><div>あおば建築設計事務所</div><div>一級建築士事務所 碧海県知事 登録第00013号</div><div>管理建築士 一級建築士 大臣登録 第000257号 白石 康晴</div></div> |  | 承認                                                                                    | 検 図                                                                                   | 作 図                                                                                   | 受付コード： 2026-0918-014 | ・ T I T L E<br><br>(仮称)ハルカゼストア 白鷺緑丘店 新築工事 | ・ N A M E<br>図面目録             |                      | 配布日 |  |
|                                  |   |  |  |  |  | 作成日： 2026 年 9 月 18 日 |                                           | ・ S C A L E<br>A1: -<br>A3: - | ・ N O.<br><br>A - 00 |     |  |
|                                  |   |  |                                                                                       |                                                                                       |                                                                                       | 工事コード： HK-2026-014   |                                           |                               |                      |     |  |

■ 設計概要

|       |                                      |
|-------|--------------------------------------|
| 工事名称  | (仮称)ハルカゼストア 白鷺緑丘店 新築工事               |
| 建 築 主 | 株式会社ハルカゼストア 代表者 大森 佳幸                |
| 所 在 地 | 碧海県白鷺市栄町二丁目5番1号                      |
| 設 計 者 | あおば建築設計事務所                           |
| 所 在 地 | 碧海県白鷺市中央三丁目1番8号                      |
| 電話番号  | 03-0000-0000    FAX 03-0000-0001     |
| 管理建築士 | 白石 康晴    (管理建築士 一級建築士 大臣登録 第000257号) |
| 担 当 者 | 早川 真澄                                |
| 建築場所  | 碧海県白鷺市緑丘三丁目14番1号                     |
| 地名地番  | 碧海県白鷺市緑丘三丁目14番1、14番2                 |
| 用途地域  | 第1種住居地域                              |
| 敷地面積  | 1,284.60 m <sup>2</sup> ( 388.59 坪 ) |
| 防火指定  | 準防火地域                                |
| 建べい率  | 指定 60 %    /    計画 17.05 %           |
| 容 積 率 | 指定 200 %    /    計画 17.05 %          |
| 前面道路  | 南側 6.0 m    (県道 白鷺緑丘線(第12号線))        |
|       | 東側 4.0 m    (市道 緑丘33-5号線)            |

■ 建築概要

|         |                                 |
|---------|---------------------------------|
| 工事種別    | 新築                              |
| 主要用途    | 物品販売業を営む店舗（食品スーパー）              |
| 構造・規模   | 鉄骨造    地上1階                     |
| 建築面積    | 219.01 m <sup>2</sup> (延べ面積 同じ) |
| 最高の高さ   | GL+5,500    (バラベット天端)           |
| 軒 の 高 さ | GL+5,400    (アルミ笠木 下端)          |
| 屋 根     | ガルバリウム鋼板 折板葺き                   |
| 外 壁     | ALCパネル t=100 縦張り    吹付塗装        |
| 外部建具    | アルミ製ほか（A-10 建具表による）             |
| 駐車台数    | 普通車 38 台    /    自転車 40 台       |

【関係法令等】

建築基準法 ・ 都市計画法 ・ 消防法 ・ 省エネ法 ・ バリアフリー法 ・ 屋外広告物法  
碧海県建築安全条例 ・ 白鷺市まちづくり条例


■ 案内図



案内図 S=1/2,500

|                                  |   |  |              |               |               |                      |                                           |                                                                        |                             |       |
|----------------------------------|---|--|--------------|---------------|---------------|----------------------|-------------------------------------------|------------------------------------------------------------------------|-----------------------------|-------|
| ・変更略歴<br>.....<br>.....<br>..... | <div><div><div></div><div>AOBA</div></div><div><div>あおば建築設計事務所</div><div>一級建築士事務所 碧海県知事 登録第00013号<br/>管理建築士 一級建築士 大臣登録 第000257号 白石 康晴</div></div></div> |  | 承認           | 検 閲           | 作 図           | 受付コード： 2026-0918-014 | ・ T I T L E<br><br>(仮称)ハルカゼストア 白鷺緑丘店 新築工事 | ・ N A M E<br>設計概要・案内図<br><br>・ S C A L E<br>A1: 1/2,500<br>A3: 1/2,500 | ・ N O.<br><br><b>A - 01</b> | 配 布 日 |
|                                  |   |  | <div>自</div> | <div>三宅</div> | <div>早川</div> | 作成日： 2026 年 9 月 18 日 |                                           |                                                                        |                             |       |
|                                  |   |  |              |               |               | 工事コード： HK-2026-014   |                                           |                                                                        |                             |       |

配置図 S=1/200

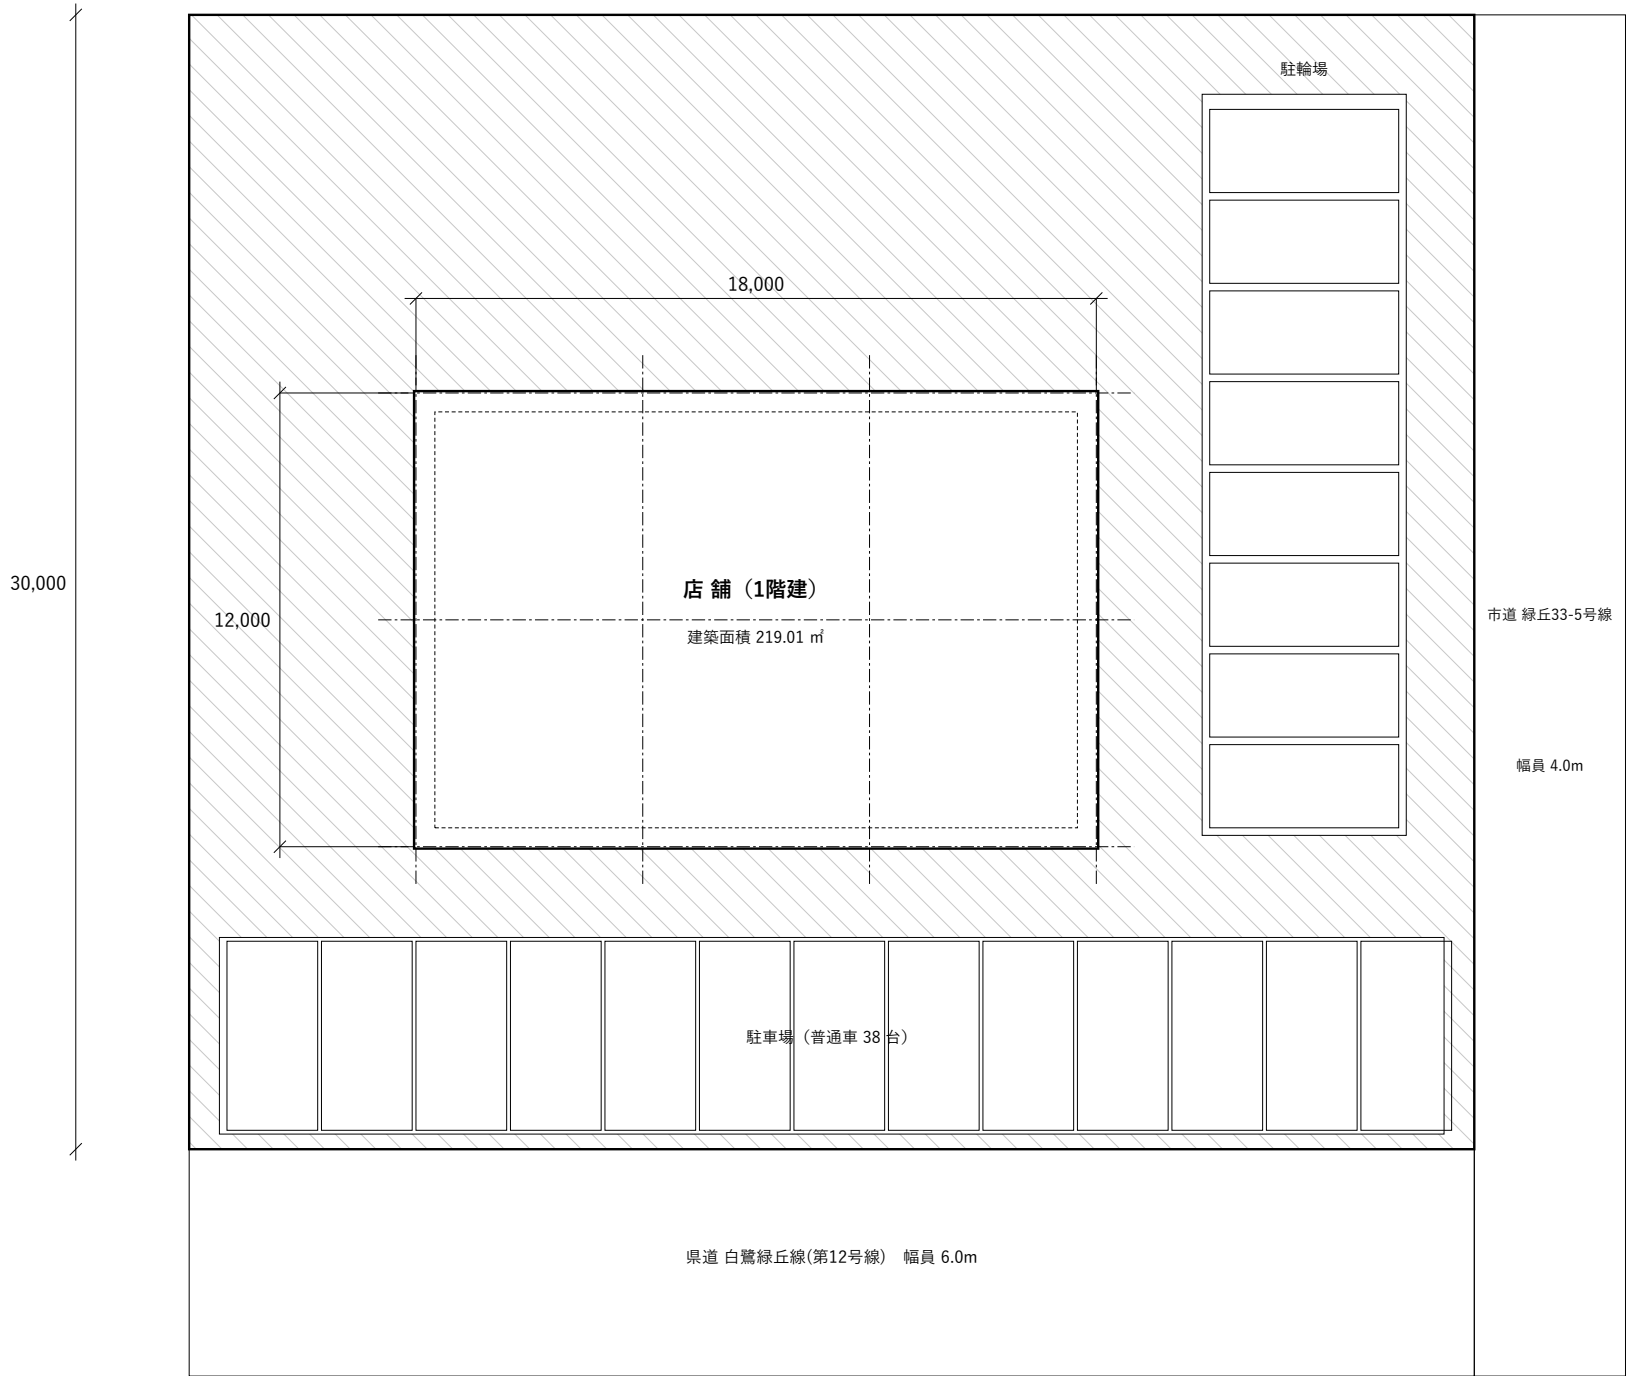

|                   |                      |
|-------------------|----------------------|
| 図名                | 配置図                  |
| 所在                | 碧海県白鷺市緑丘三丁目14番1号     |
| 地番                | 碧海県白鷺市緑丘三丁目14番1、14番2 |
| 碧海県白鷺市中央三丁目1番8号   |                      |
| あおば建築設計事務所        |                      |
| 一級建築士・管理建築士 白石 康晴 |                      |
| TEL 03-0000-0000  | FAX 03-0000-0001     |
| 担当 早川 真澄          |                      |

特記仕様書

|      |                        |
|------|------------------------|
| 工事名称 | (仮称)ハルカゼストア 白鷺緑丘店 新築工事 |
| 建築場所 | 碧海県白鷺市緑丘三丁目14番1号       |
| 発注者  | ハルカゼストア 様              |
| 設計者  | あおば建築設計事務所             |
| 監理者  | あおば建築設計事務所 早川 真澄       |

1. 一般事項

- 1-1 本仕様書は、上記工事に適用する。記載のない事項は公共建築工事標準仕様書（建築工事編）による。
- 1-2 図面と本仕様書の内容が食い違う場合は、監理者に確認のうえ指示を受ける。
- 1-3 工事に先立ち、施工計画書・施工図・見本を提出し、監理者の承認を受ける。
- 1-4 材料は原則として日本産業規格（JIS）に適合するものとする。

2. 仮設工事

- 2-1 仮囲いは高さ3.0m以上とし、出入口には扉を設ける。
- 2-2 敷地境界の確認は着工前に行き、隣地との立会い結果を書面で残す。
- 2-3 工事用電力・用水は施工者の負担とする。

3. 土工事・地業工事

- 3-1 根切り底は地盤調査報告書の支持層を確認のうえ、監理者の検査を受ける。
- 3-2 埋戻し土は良質土とし、300mmごとに転圧する。
- 3-3 捨てコンクリートは Fc18、厚さ50mmとする。

4. 鉄骨工事

- 4-1 使用鋼材は SN400B とし、ミルシートを提出する。
- 4-2 溶接は工場溶接を原則とし、全溶接部の10%以上について超音波探傷試験を行う。
- 4-3 アンカーボルトの心ずれは5mm以内とする。
- 4-4 錆止め塗装は2回塗りとし、耐火被覆部は除く。

5. 外装工事

- 5-1 ALCパネルは厚さ100mm、縦張りとし、取付金物はロッキング構法とする。
- 5-2 目地はシーリング（変成シリコーン系）とし、幅10mm・深さ8mmを標準とする。
- 5-3 屋根はガルバリウム鋼板 t=0.6 折板葺きとし、勾配は1/50とする。
- 5-4 バラベット天端はアルミ笠木とし、下端をGL+5,400とする。

6. 建具工事

- 6-1 外部アルミ建具は A-10 建具表による。耐風圧性能は 2,400Pa 以上とする。
- 6-2 自動ドアは光電式センサーとし、停電時は手動で開放できるものとする。
- 6-3 鋼製建具の板厚は t=1.6 を標準とする。

7. 内装工事

- 7-1 天井はロックウール吸音板 t=9 とし、下地は軽量鉄骨とする。
- 7-2 売場の床は塩ビ長尺シート t=2.0 とし、下地はコンクリート金ゴテ押えとする。
- 7-3 バックヤードの床は防塵塗装（エポキシ樹脂系）2回塗りとする。
- 7-4 内装制限のかかる部分は不燃材料とし、認定番号を提出する。

8. 外構工事

- 8-1 駐車場の舗装はアスファルト t=50、路盤 t=150 とする。
- 8-2 区画線は白色・幅100とし、車椅子使用者用駐車施設を1台分設ける。
- 8-3 雨水は敷地内の浸透ますで処理する。放流先は監理者の指示による。
- 8-4 植栽は在来種を用い、活着まで施工者が管理する。

9. 提出書類

- 9-1 完成時に、竣工図・保証書・取扱説明書を各2部提出する。
- 9-2 主要材料の試験成績書は、使用前に監理者へ提出する。
- 9-3 工事写真は工種ごとに撮影し、電子データで提出する。

【 質疑・確認の窓口 】

あおば建築設計事務所 担当 早川 真澄      電話番号 03-0000-0000      FAX 03-0000-0001

碧海県白鷺市中央三丁目1番8号

|                                                      |   |  |                      |                        |    |                      |                                      |                |  |     |
|------------------------------------------------------|---|--|----------------------|------------------------|----|----------------------|--------------------------------------|----------------|--|-----|
| <div>・変更略歴</div> <div></div> <div></div> <div></div> | <div><div><div><div></div><div>AOBA</div></div><div><div>あおば建築設計事務所</div><div>一級建築士事務所 岩海県知事 登録第00013号</div><div>管理建築士 一級建築士 大臣登録 第000257号 白石 康晴</div></div></div></div> |  | 承認                   | 検図                     | 作図 | 受付コード： 2026-0918-014 | ・TITLE<br><br>(仮称)ハルカゼストア 白鷺緑丘店 新築工事 | ・NAME<br>特記仕様書 |  | 配布日 |
|                                                      |   |  | 作成日： 2026 年 9 月 18 日 | ・SCALE<br>A1:-<br>A3:- |    |                      |                                      |                |  |     |
|                                                      |   |  | 工事コード： HK-2026-014   | ・NO.<br><br>A - 03     |    |                      |                                      |                |  |     |
|                                                      |   |  | <div>白</div>         |                        |    | <div>三宅</div>        |                                      | <div>早川</div>  |  |     |

外部仕上表

工事名称（仮称）ハルカゼストア 白鷺緑丘店 新築工事

設計 あおば建築設計事務所

建築場所 碧海県白鷺市緑丘三丁目14番1号

担当 早川 真澄

| 部 位      | 下 地              | 仕 上                  | 備 考                      |
|----------|------------------|----------------------|--------------------------|
| 屋 根      | 折板受けタイトフレーム      | ガルバリウム鋼板 t=0.6 折板葺き  | 勾配 1/50 ・ けらば包み共         |
| バラベツ天端   | ALCパネル t=100     | アルミ笠木（シルバーアルマイト）     | 下端 GL+5,400              |
| 外 壁（一般部） | ALCパネル t=100 縦張り | 複層塗材E 吹付（アイボリー）      | 目地 変成シリコーン               |
| 外 壁（腰 壁） | ALCパネル t=100     | 複層塗材E 吹付（ダークグレー）     | GL+900 まで                |
| 軒 天 井    | 軽量鉄骨下地           | ケイ酸カルシウム板 t=6 + EP塗装 | 入口廻りのみ                   |
| 外部建具     | －                | アルミ製・鋼製（A-10 建具表による） | AD-1／AW-1／AW-2／SD-1／SS-1 |
| シャッター    | －                | スチール製 軽量シャッター 電動     | 搬入口 SS-1                 |
| 外部床（歩道部） | 碎石＋砂             | インターロッキングブロック t=60   | 駐車場出入口は t=80             |
| 外部床（駐車場） | 路盤 t=150         | アスファルト舗装 t=50        | 区画線 白色 幅100              |
| 樋 ・ 排 水  | －                | 硬質塩ビ VP75（内樋・たて樋）    | 排水は敷地内浸透ますへ              |
| 換気ガラリ    | ALCパネル開口         | アルミ製 ガラリ 600×400     | 北面 2箇所・FL+4,000          |
| 外部サイン    | －                | 別途工事                 | 位置は監理者の指示による             |

注1) 色は別途 色見本により監理者の承認を受ける。

注2) 本表に記載のない部位は、特記仕様書（A-03）による。

注3) 換気ガラリは建具表に含まない。符号は現場にて監理者と取り決める。

・変更略歴



あおば建築設計事務所

一級建築士事務所 碧海県知事 登録第00013号

管理建築士 一級建築士 大臣登録 第000257号 白石 康晴

承認

白石

検 図

三宅

作 図

早川

受付コード： 2026-0918-014

作成日： 2026 年 9 月 18 日

工事コード： HK-2026-014

・TITLE

(仮称)ハルカゼストア 白鷺緑丘店 新築工事

・NAME

外部仕上表


・SCALE

A1:-  
A3:-


・NO.

A - 04

配布日

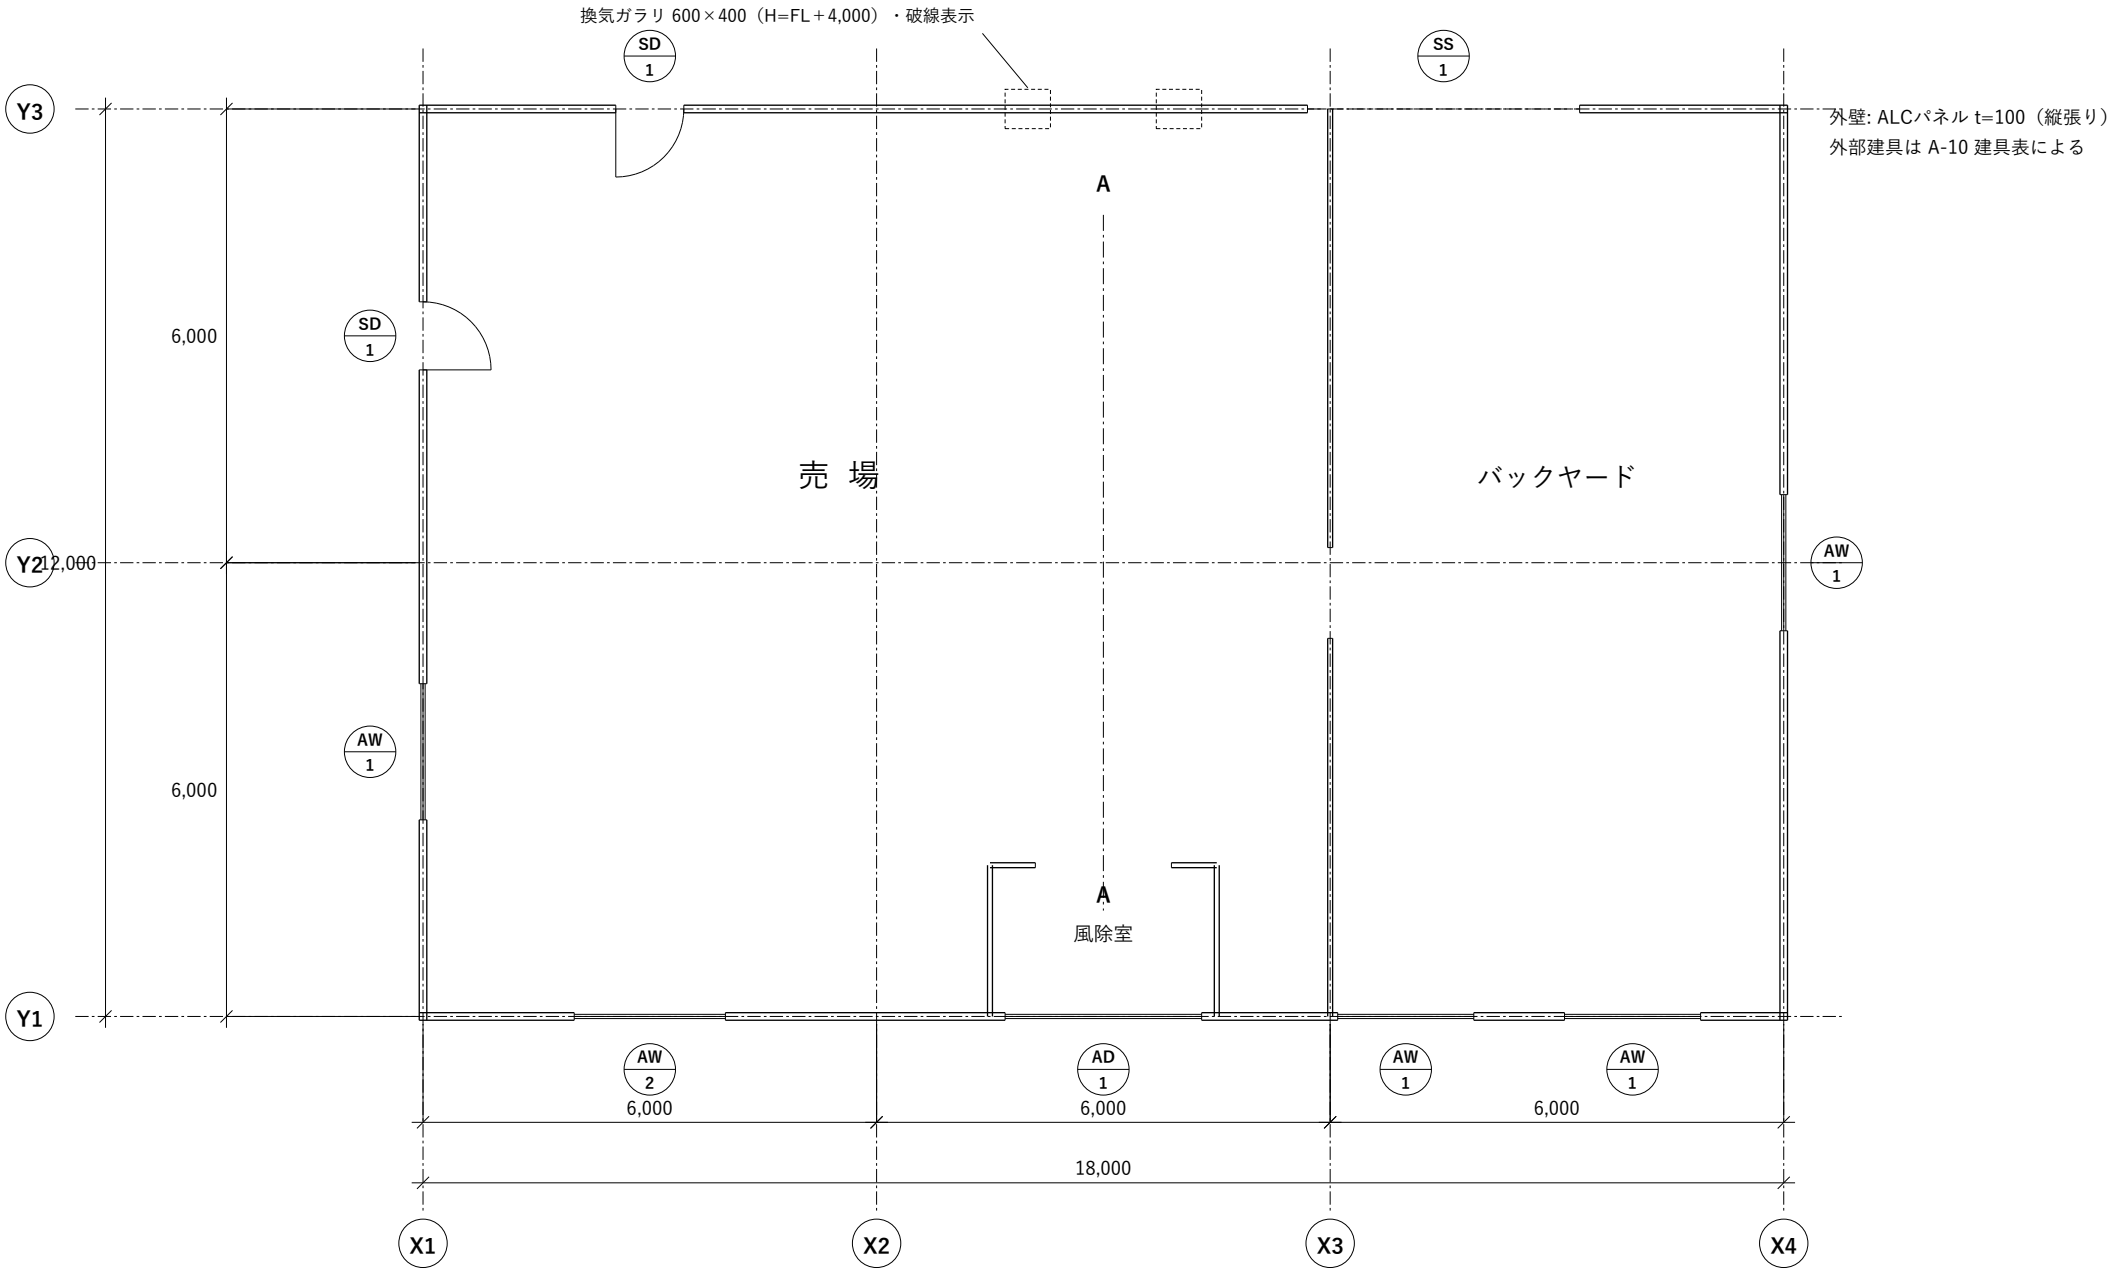


|                                  |   |  |                                                                                       |                                                                                       |                                                                                       |                      |                                      |                                 |  |     |  |
|----------------------------------|---|--|---------------------------------------------------------------------------------------|---------------------------------------------------------------------------------------|---------------------------------------------------------------------------------------|----------------------|--------------------------------------|---------------------------------|--|-----|--|
| ・変更略歴<br>.....<br>.....<br>..... |  <b>あおば建築設計事務所</b><br>一級建築士事務所 岩手県知事 登録第00013号<br>管理建築士 一級建築士 大臣登録 第000257号 白石 康晴 |  | 承認                                                                                    | 検図                                                                                    | 作図                                                                                    | 受付コード： 2026-0918-014 | ・TITLE<br><br>(仮称)ハルカゼストア 白鷺緑丘店 新築工事 | ・NAME<br><b>1階平面図</b>           |  | 配布日 |  |
|                                  |   |  |  |  |  | 作成日： 2026 年 9 月 18 日 |                                      | ・SCALE<br>A1: 1/50<br>A3: 1/100 |  |     |  |
|                                  |   |  |                                                                                       |                                                                                       |                                                                                       | 工事コード： HK-2026-014   |                                      |                                 |  |     |  |
|                                  |   |  |                                                                                       |                                                                                       |                                                                                       |                      |                                      |                                 |  |     |  |
|                                  |   |  |                                                                                       |                                                                                       |                                                                                       |                      |                                      | ・NO.<br><b>A - 05</b>           |  |     |  |

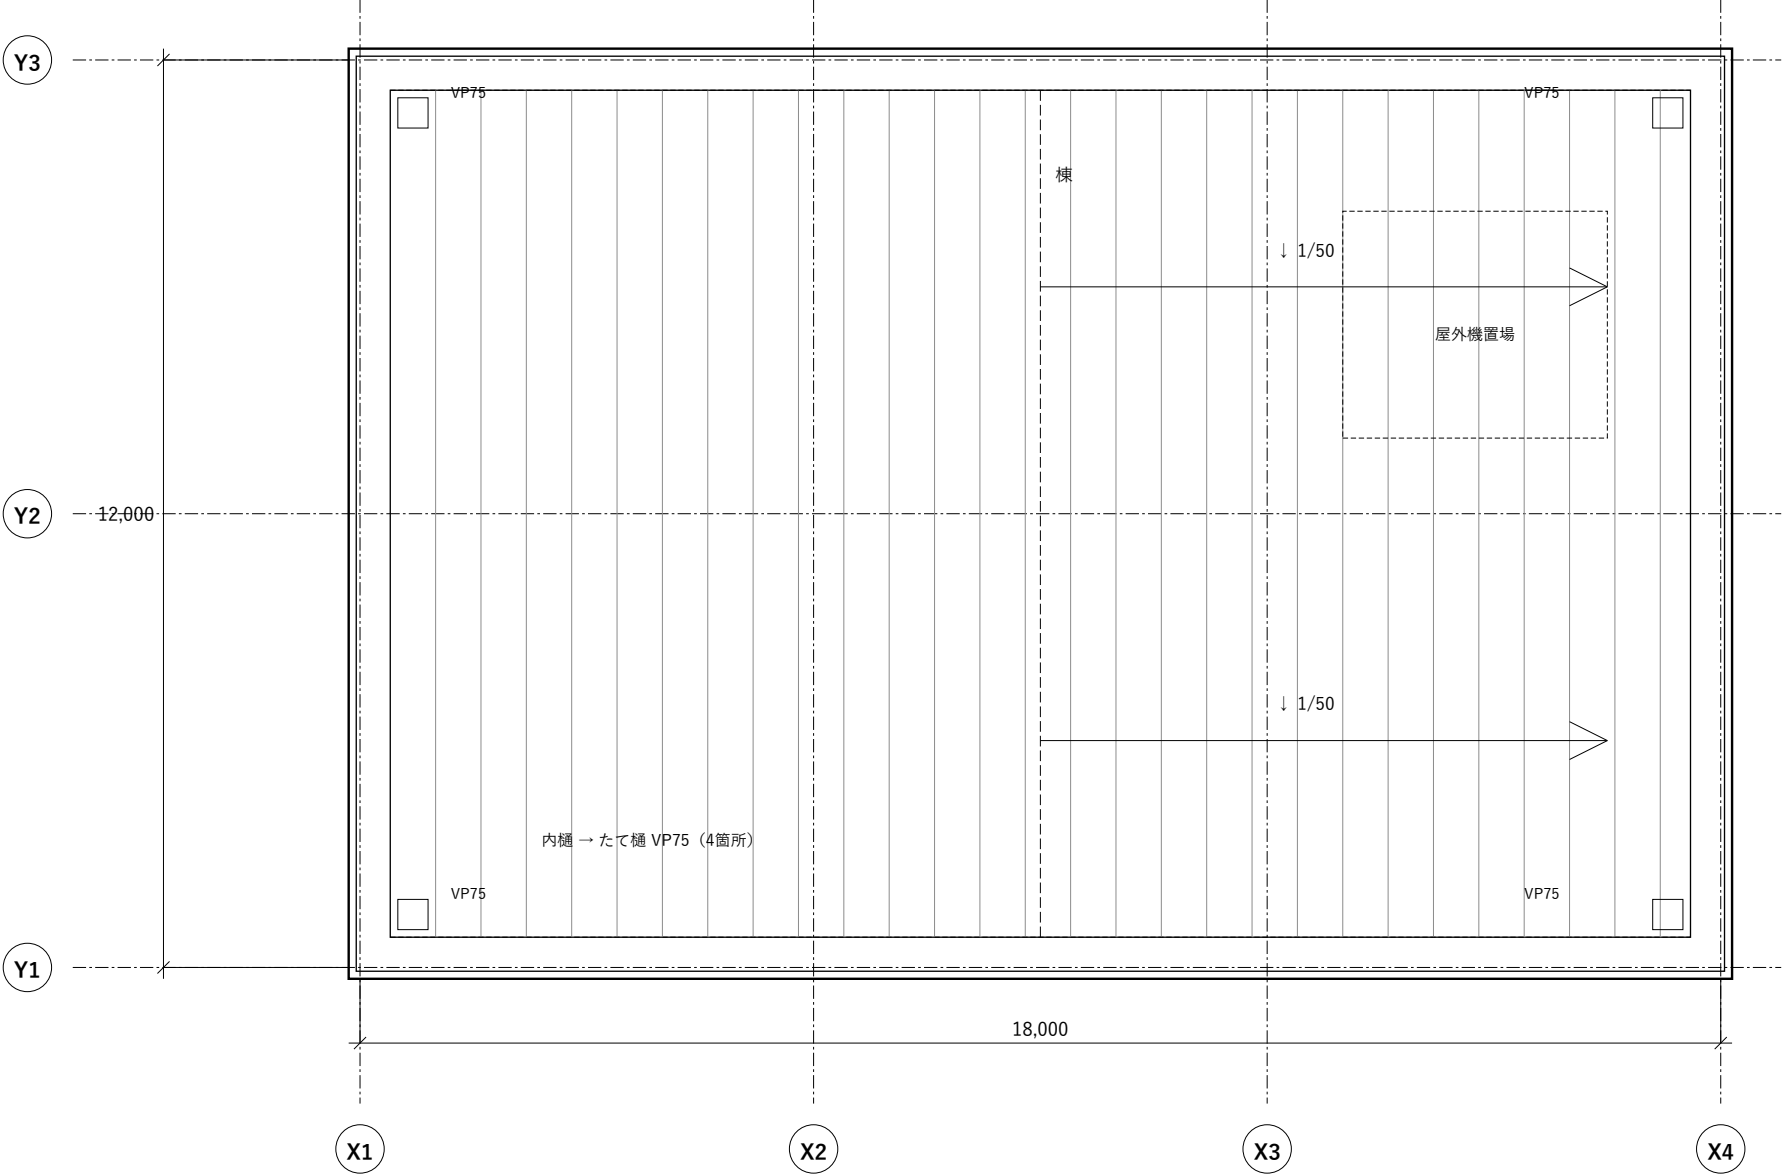


屋根: ガルバリウム鋼板 t=0.6 折板葺き (勾配 1/50)  
パラベット天端 GL+5,500 / アルミ笠木 下端 GL+5,400  
屋上の設備置場は別途工事とし、荷重は構造図による。




|                                  |   |  |                      |                                 |                    |                      |                                      |               |  |     |
|----------------------------------|---|--|----------------------|---------------------------------|--------------------|----------------------|--------------------------------------|---------------|--|-----|
| ・変更略歴<br>.....<br>.....<br>..... | <div><div><div>あおば建築設計事務所</div><div>一級建築士事務所 碧海県知事 登録第00013号</div><div>管理建築士 一級建築士 大臣登録 第000257号 白石 康晴</div></div></div> |  | 承認                   | 検図                              | 作図                 | 受付コード： 2026-0918-014 | ・TITLE<br><br>(仮称)ハルカゼストア 白鷺緑丘店 新築工事 | ・NAME<br>屋根伏図 |  | 配布日 |
|                                  |   |  | 作成日： 2026 年 9 月 18 日 | ・SCALE<br>A1: 1/50<br>A3: 1/100 | ・NO.<br><br>A - 06 |                      |                                      |               |  |     |
|                                  |   |  | 工事コード： HK-2026-014   |                                 |                    |                      |                                      |               |  |     |
|                                  |   |  |                      |                                 |                    |                      |                                      |               |  |     |

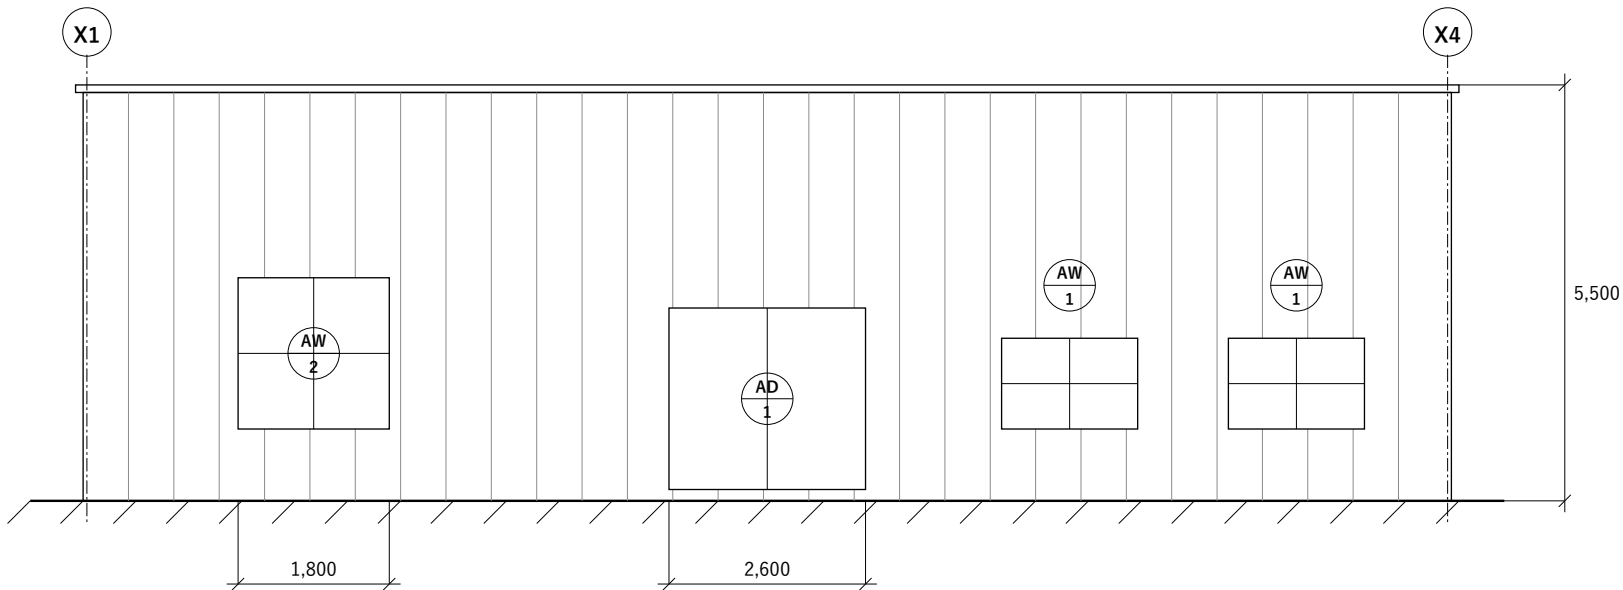

南立面図 S=1/100

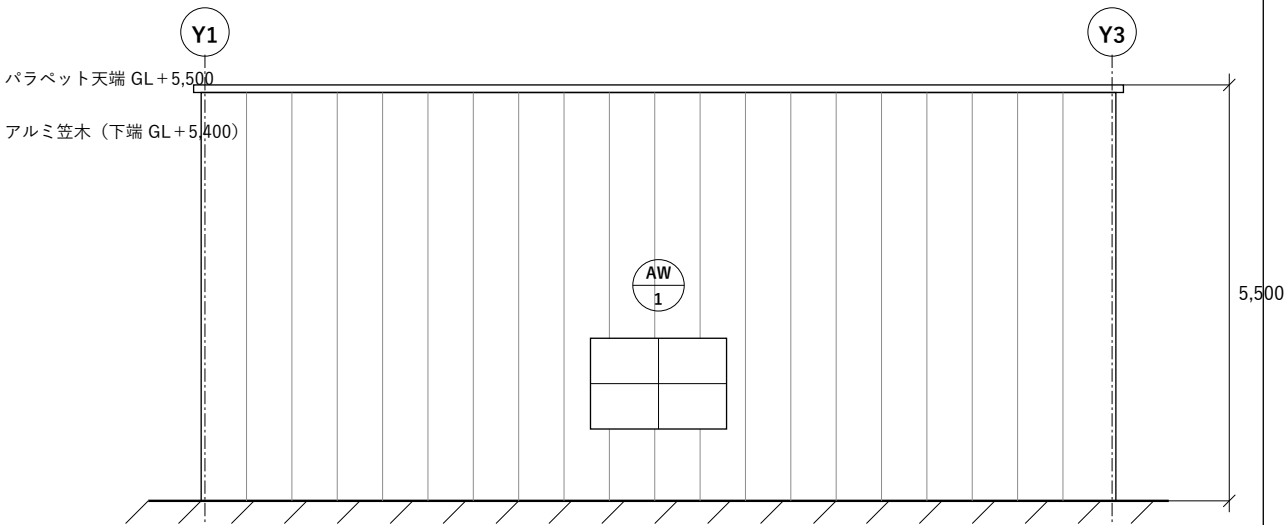


東立面図 S=1/100

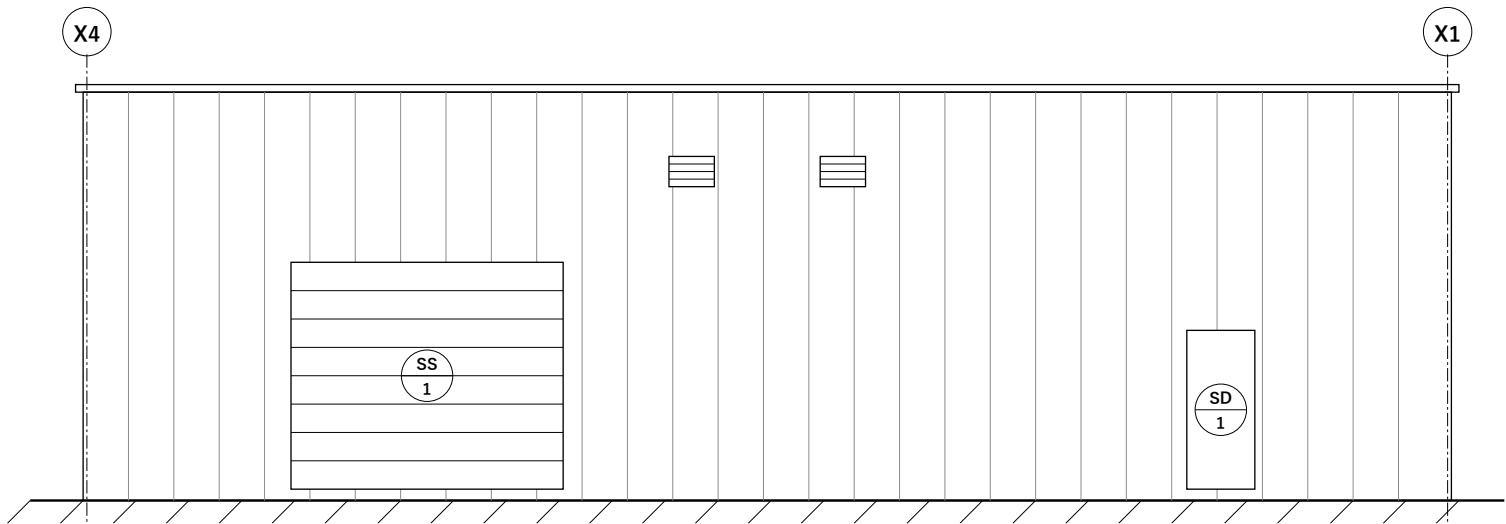

北立面図 S=1/100

外壁仕上は A-04 外部仕上表による。開口の寸法は A-10 建具表による。

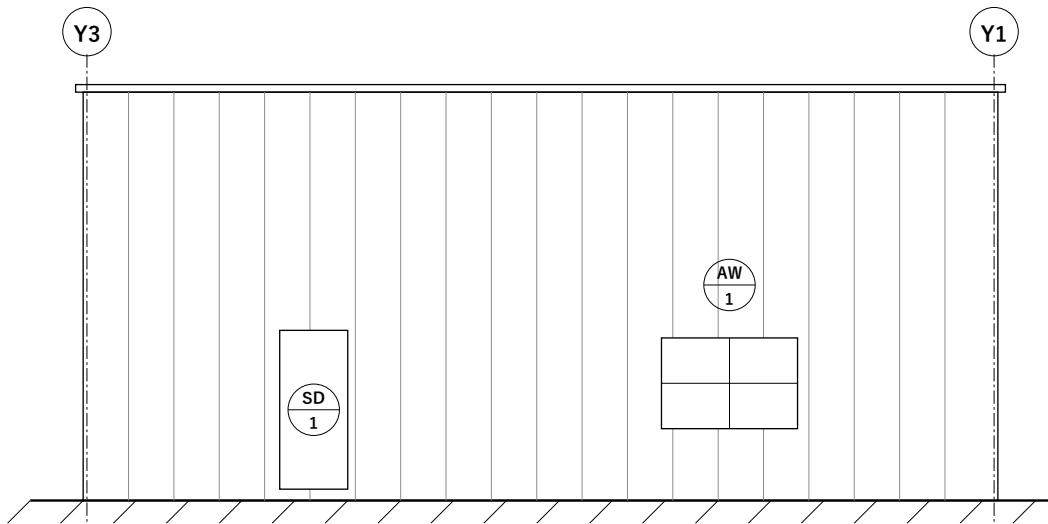


西立面図 S=1/100

|                                  |   |  |                                                                                       |                                                                                       |                                                                                       |                      |                                      |                                 |                    |     |
|----------------------------------|---|--|---------------------------------------------------------------------------------------|---------------------------------------------------------------------------------------|---------------------------------------------------------------------------------------|----------------------|--------------------------------------|---------------------------------|--------------------|-----|
| ・変更略歴<br>.....<br>.....<br>..... | <div><p>あおば建築設計事務所</p><p>一級建築士事務所 岩海県知事 登録第00013号</p><p>管理建築士 一級建築士 大臣登録 第000257号 白石 康晴</p></div> |  | 承認                                                                                    | 検図                                                                                    | 作図                                                                                    | 受付コード： 2026-0918-014 | ・TITLE<br><br>(仮称)ハルカゼストア 白鷺緑丘店 新築工事 | ・NAME<br>立面図(東西南北)              |                    | 配布日 |
|                                  |   |  |  |  |  | 作成日： 2026 年 9 月 18 日 |                                      | ・SCALE<br>A1: 1/50<br>A3: 1/100 | ・NO.<br><br>A - 07 |     |
|                                  |   |  |                                                                                       |                                                                                       |                                                                                       | 工事コード： HK-2026-014   |                                      |                                 |                    |     |
|                                  |   |  |                                                                                       |                                                                                       |                                                                                       |                      |                                      |                                 |                    |     |


A - A' 断面図 S=1/100

切断位置は A-05 1階平面図による

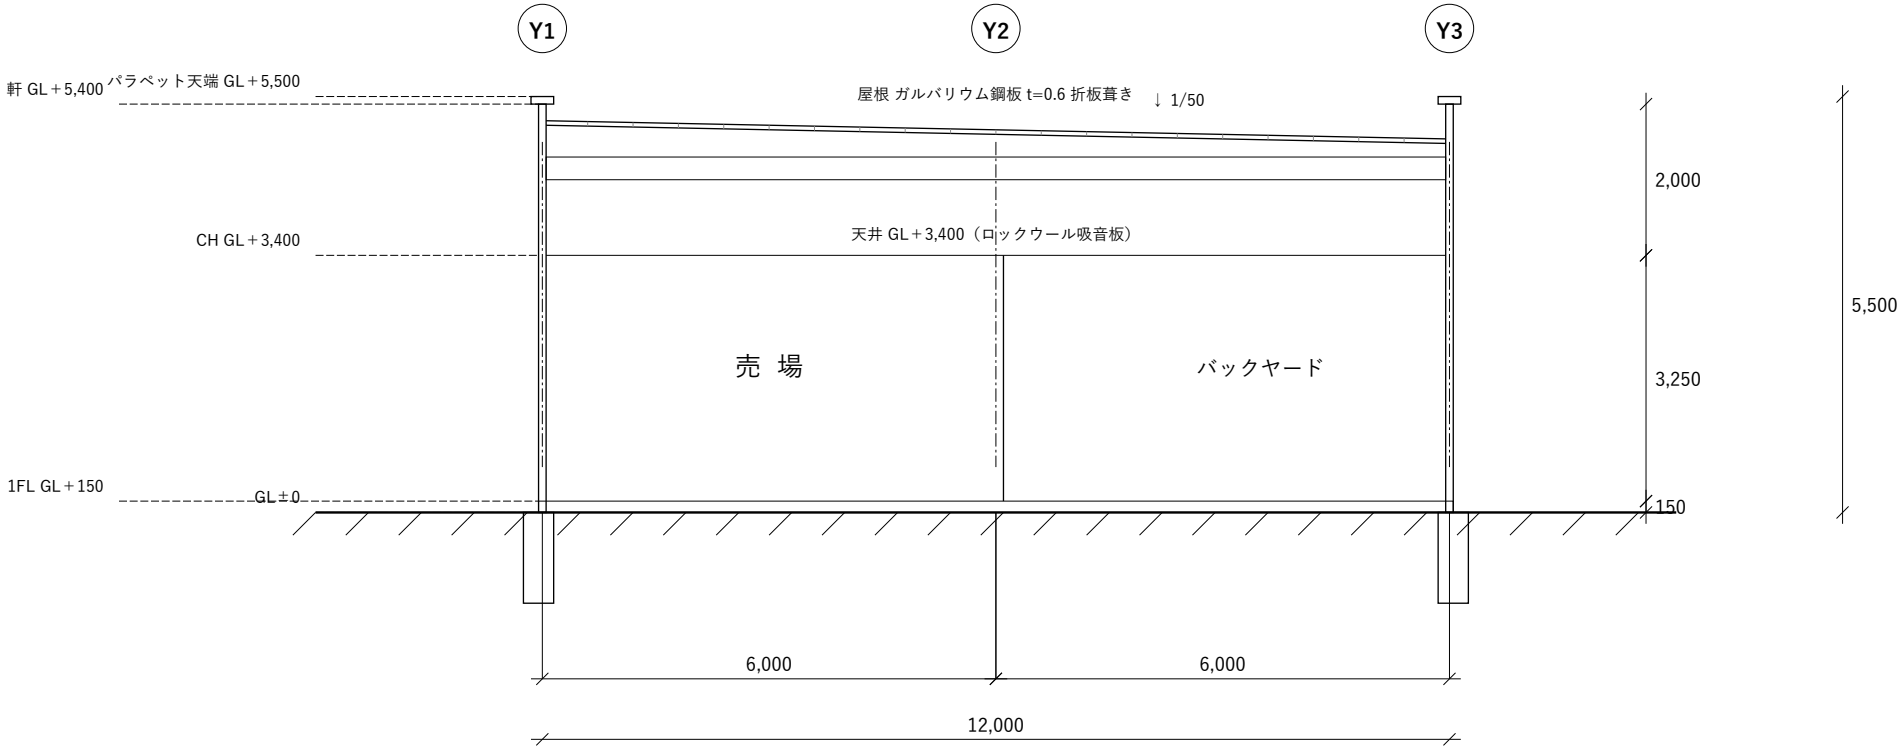

構造は鉄骨造。柱・梁の断面は構造図（別途）による。  
断熱は屋根面 グラスウール t=100、外壁面 ALCパネルによる。

|                                                      |   |  |              |              |              |                      |                                                     |                                                     |                                   |                |
|------------------------------------------------------|---|--|--------------|--------------|--------------|----------------------|-----------------------------------------------------|-----------------------------------------------------|-----------------------------------|----------------|
| <div>・変更略歴</div> <div></div> <div></div> <div></div> | <div><div><div><div></div></div><div>AOBA</div></div><div><div>あおば建築設計事務所</div><div>一級建築士事務所 岩手県知事 登録第00013号</div><div>管理建築士 一級建築士 大臣登録 第000257号 白石 康晴</div></div></div> |  | 承認           | 検図           | 作図           | 受付コード： 2026-0918-014 | <div>・TITLE</div> <div>(仮称)ハルカゼストア 白鷺緑丘店 新築工事</div> | <div>・NAME</div> <div>断面図</div>                     |                                   | <div>配布日</div> |
|                                                      |   |  | <div>白</div> | <div>三</div> | <div>早</div> | 作成日： 2026 年 9 月 18 日 |                                                     | <div>・SCALE</div> <div>A1: 1/50<br/>A3: 1/100</div> | <div>・NO.</div> <div>A - 08</div> |                |
|                                                      |   |  |              |              |              | 工事コード： HK-2026-014   |                                                     |                                                     |                                   |                |
|                                                      |   |  |              |              |              |                      |                                                     |                                                     |                                   |                |

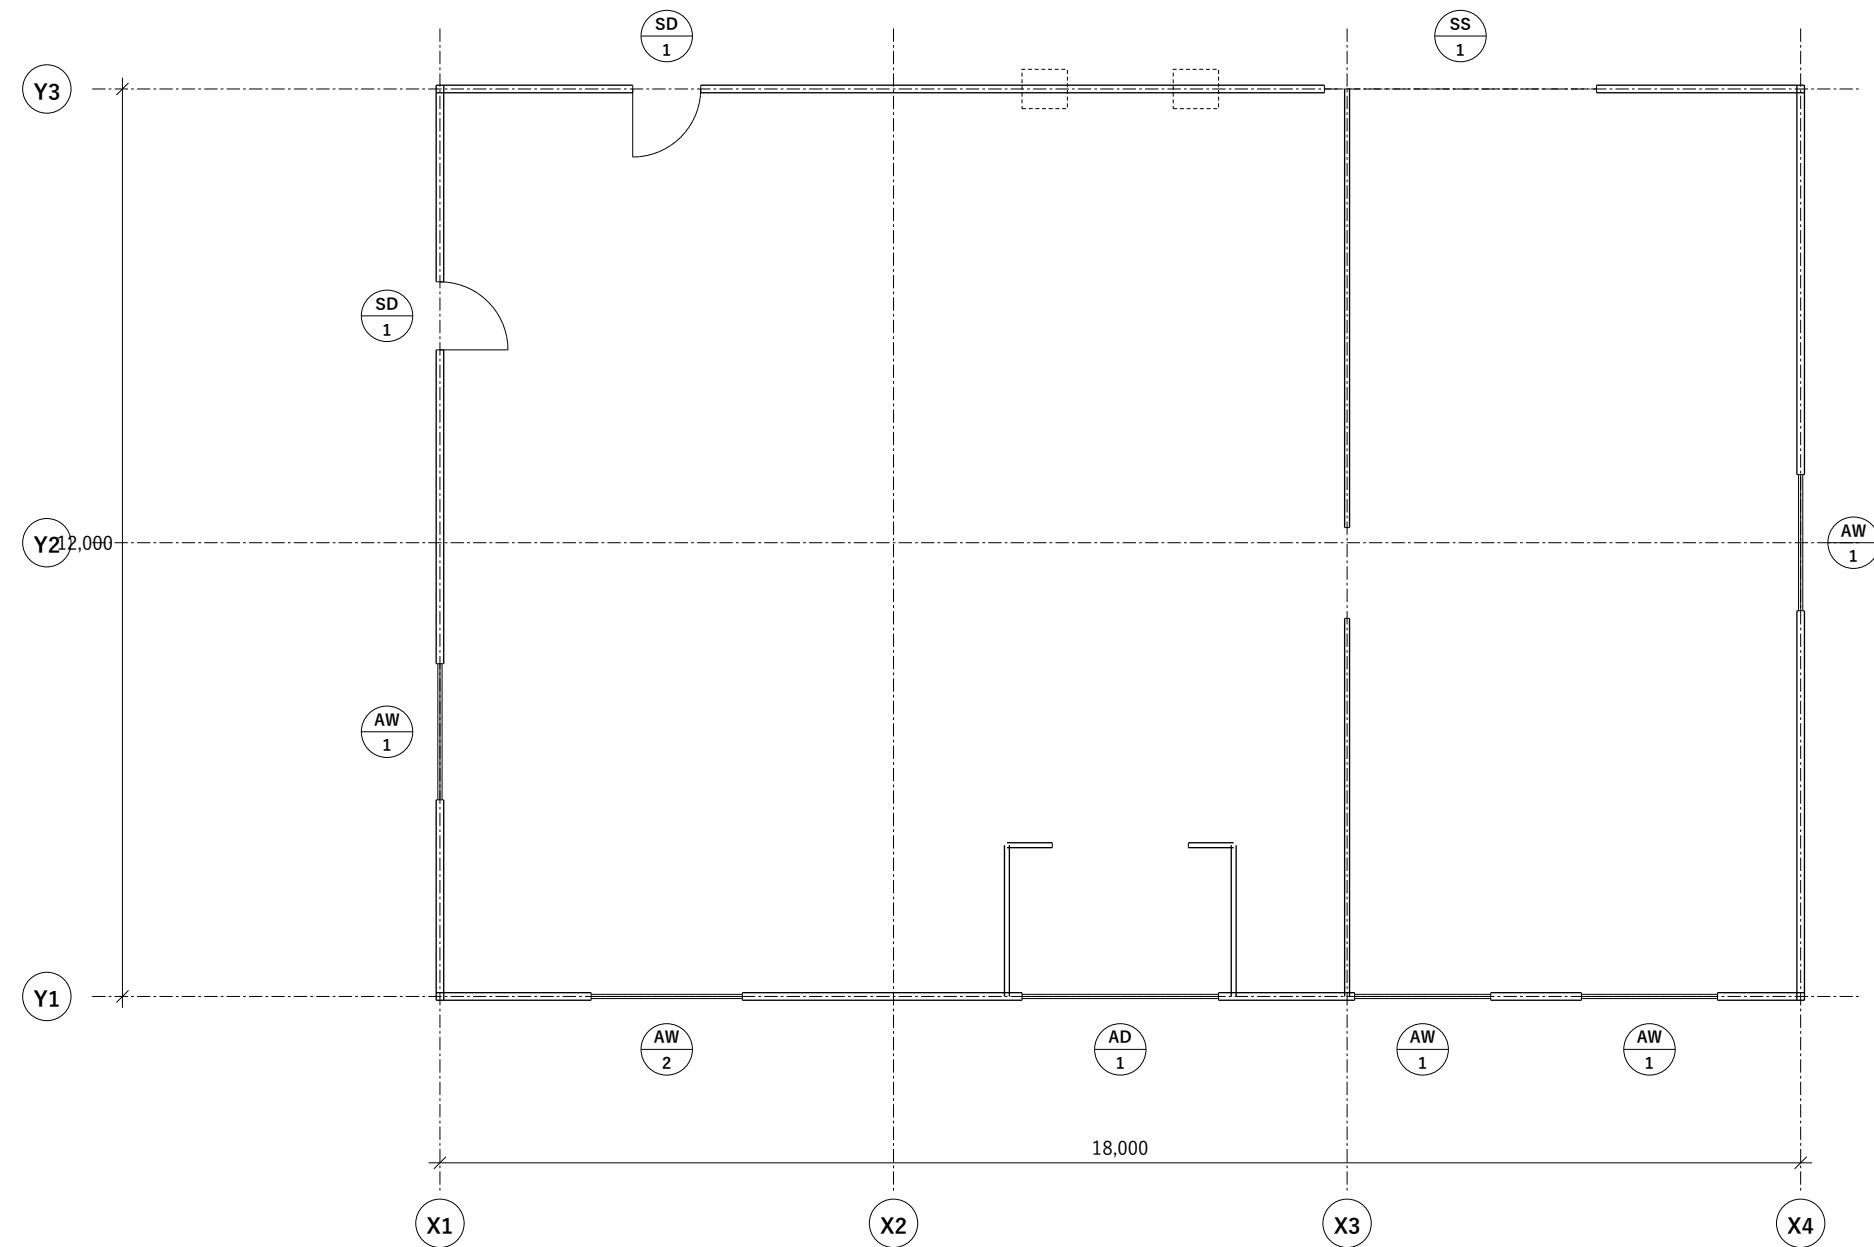

建具の位置

| 符号     | 面 | 位置（通り芯）   | 数量 |
|--------|---|-----------|----|
| AD-1   | 南 | X芯 9,000  | 1  |
| AW-2   | 南 | X芯 3,000  | 1  |
| AW-1   | 南 | X芯 13,000 | 1  |
| AW-1   | 南 | X芯 16,000 | 1  |
| SD-1   | 北 | X芯 3,000  | 1  |
| (符号なし) | 北 | X芯 8,000  | 1  |
| (符号なし) | 北 | X芯 10,000 | 1  |
| SS-1   | 北 | X芯 13,500 | 1  |
| AW-1   | 東 | Y芯 6,000  | 1  |
| AW-1   | 西 | Y芯 3,500  | 1  |
| SD-1   | 西 | Y芯 9,000  | 1  |

※ 換気ガラリ（600×400）は建具表に無い。





符号は監理者（早川 真澄）の指示による。



建 具 表（外部建具）

工事名称（仮称）ハルカゼストア 白鷺緑丘店 新築工事

設計 あおば建築設計事務所 / 担当 早川 真澄
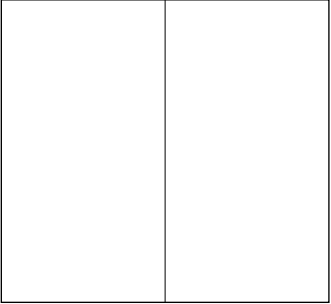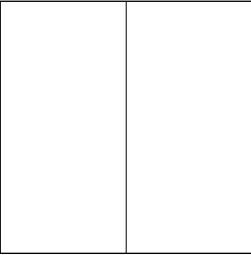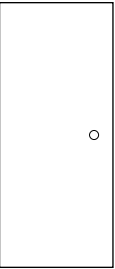 
|        |   |   |   |   |   |
|--------|---|---|---|---|---|
| 符号     | <div>AD<br/>1</div>                                                                                            | <div>AW<br/>1</div>                                                                                        | <div>AW<br/>2</div>                                                                                          | <div>SD<br/>1</div>                                                                                         | <div>SS<br/>1</div>                                                                                            |
| 姿図     | <div><p>(自動ドア(引分け))</p></div> | <div><p>(引違い窓)</p></div> | <div><p>(はめ殺し窓)</p></div> | <div><p>(片開き扉)</p></div> | <div><p>(軽量シャッター)</p></div> |
| 寸法 W×H | 2,600 × 2,400                                                                                                  | 1,800 × 1,200                                                                                              | 2,000 × 2,000                                                                                                | 900 × 2,100                                                                                                 | 3,600 × 3,000                                                                                                  |
| 数量     | 1 箇所   | 4 箇所   | 1 箇所   | 2 箇所   | 1 箇所   |
| 材質・仕上  | アルミ製   | アルミ製   | アルミ製   | 鋼製フラッシュ   | スチール製・電動   |
| ガラス    | 強化ガラス t=10   | 複層ガラス   | 複層ガラス   | -   | -   |
| 備考     | 正面入口・風除室   | 網戸付   | -   | 錠前付   | 搬入口   |

注1) 寸法は内法基準の呼称寸法とする。取合いの詳細は施工図による。  
注2) 本表は外部建具を示す。位置は A-09 建具キープランによる。  
注3) 変更が生じた場合は あおば建築設計事務所（電話番号 03-0000-0000 担当 早川 真澄）まで連絡すること。