

(仮称)ハルカゼストア 白鷺緑丘店 新築工事

建 築 図

建 築 主	株式会社ハルカゼストア （ハルカゼストア 様）
所 在 地	碧海県白鷺市栄町二丁目5番1号
設 計 者	あおば建築設計事務所 一級建築士事務所 碧海県知事 登録第00013号
所 在 地	碧海県白鷺市中央三丁目1番8号 電話番号 03-0000-0000 FAX 03-0000-0001
管理建築士	白石 康晴
担 当 者	早川 真澄
建築場所	碧海県白鷺市緑丘三丁目14番1号
作 成 日	2026 年 9 月 18 日

図 面 リ ス ト

図面番号	図 面 名	縮尺(A1)	縮尺(A3)	備 考
A-00	図面目録	-	-	
A-01	設計概要・案内図	1/2,500	1/2,500	案内図を含む
A-02	配置図	1/200	1/200	
A-03	特記仕様書	-	-	共通仕様は本書による
A-04	外部仕上表	-	-	
A-05	1階平面図	1/50	1/100	
A-06	屋根伏図	1/50	1/100	
A-07	立面図(東西南北)	1/50	1/100	
A-08	断面図	1/50	1/100	
A-09	建具キープラン	1/50	1/100	建具符号の位置
A-10	建具表	1/30	1/60	外部建具

【 注 意 】
この図面は架空の物件です。実在の物件・団体・人物とは関係ありません。
PDFマスクツールの動きを見せるためのサンプルです。

・変更略歴	 あおば建築設計事務所 一級建築士事務所 碧海県知事 登録第00013号 管理建築士 一級建築士 大臣登録 第000257号 白石 康晴		承認 	検 図 	作 図 	受付コード： 2026-0918-014 作成日： 2026 年 9 月 18 日 工事コード： HK-2026-014	・ T I T L E (仮称)ハルカゼストア 白鷺緑丘店 新築工事	・ N A M E 図面目録 ・ S C A L E A1: - A3: -	・ N O. A - 00	配布日
----------------------------------	---	--	---	--	--	--	---	--	----------------------	-----

■ 設計概要

工事名称	(仮称)ハルカゼストア 白鷺緑丘店 新築工事
建 築 主	株式会社ハルカゼストア 代表者 大森 佳幸
所 在 地	碧海県白鷺市栄町二丁目5番1号
設 計 者	あおば建築設計事務所
所 在 地	碧海県白鷺市中央三丁目1番8号
電話番号	03-0000-0000 FAX 03-0000-0001
管理建築士	白石 康晴 (管理建築士 一級建築士 大臣登録 第000257号)
担 当 者	早川 真澄
建築場所	碧海県白鷺市緑丘三丁目14番1号
地名地番	碧海県白鷺市緑丘三丁目14番1、14番2
用途地域	第1種住居地域
敷地面積	1,284.60 m ² (388.59 坪)
防火指定	準防火地域
建べい率	指定 60 % / 計画 17.05 %
容 積 率	指定 200 % / 計画 17.05 %
前面道路	南側 6.0 m (県道 白鷺緑丘線(第12号線))
	東側 4.0 m (市道 緑丘33-5号線)

■ 建築概要

工事種別	新築
主要用途	物品販売業を営む店舗（食品スーパー）
構造・規模	鉄骨造 地上1階
建築面積	219.01 m ² (延べ面積 同じ)
最高の高さ	GL+5,500 (バラベット天端)
軒 の 高 さ	GL+5,400 (アルミ笠木 下端)
屋 根	ガルバリウム鋼板 折板葺き
外 壁	ALCパネル t=100 縦張り 吹付塗装
外部建具	アルミ製ほか（A-10 建具表による）
駐車台数	普通車 38 台 / 自転車 40 台

【 関係法令等 】

建築基準法 ・ 都市計画法 ・ 消防法 ・ 省エネ法 ・ バリアフリー法 ・ 屋外広告物法
碧海県建築安全条例 ・ 白鷺市まちづくり条例


■ 案内図



案内図 S=1/2,500

・変更略歴	AOBA あおば建築設計事務所 一級建築士事務所 碧海県知事 登録第00013号 管理建築士 一級建築士 大臣登録 第000257号 白石 康晴		承認	検 閲	作 図	受付コード： 2026-0918-014	・ T I T L E (仮称)ハルカゼストア 白鷺緑丘店 新築工事	・ N A M E 設計概要・案内図		配布日
			自	三宅	早川	作成日： 2026 年 9 月 18 日		・ S C A L E A1: 1/2,500 A3: 1/2,500	・ N O. A - 01	
						工事コード： HK-2026-014				

配置図 S=1/200

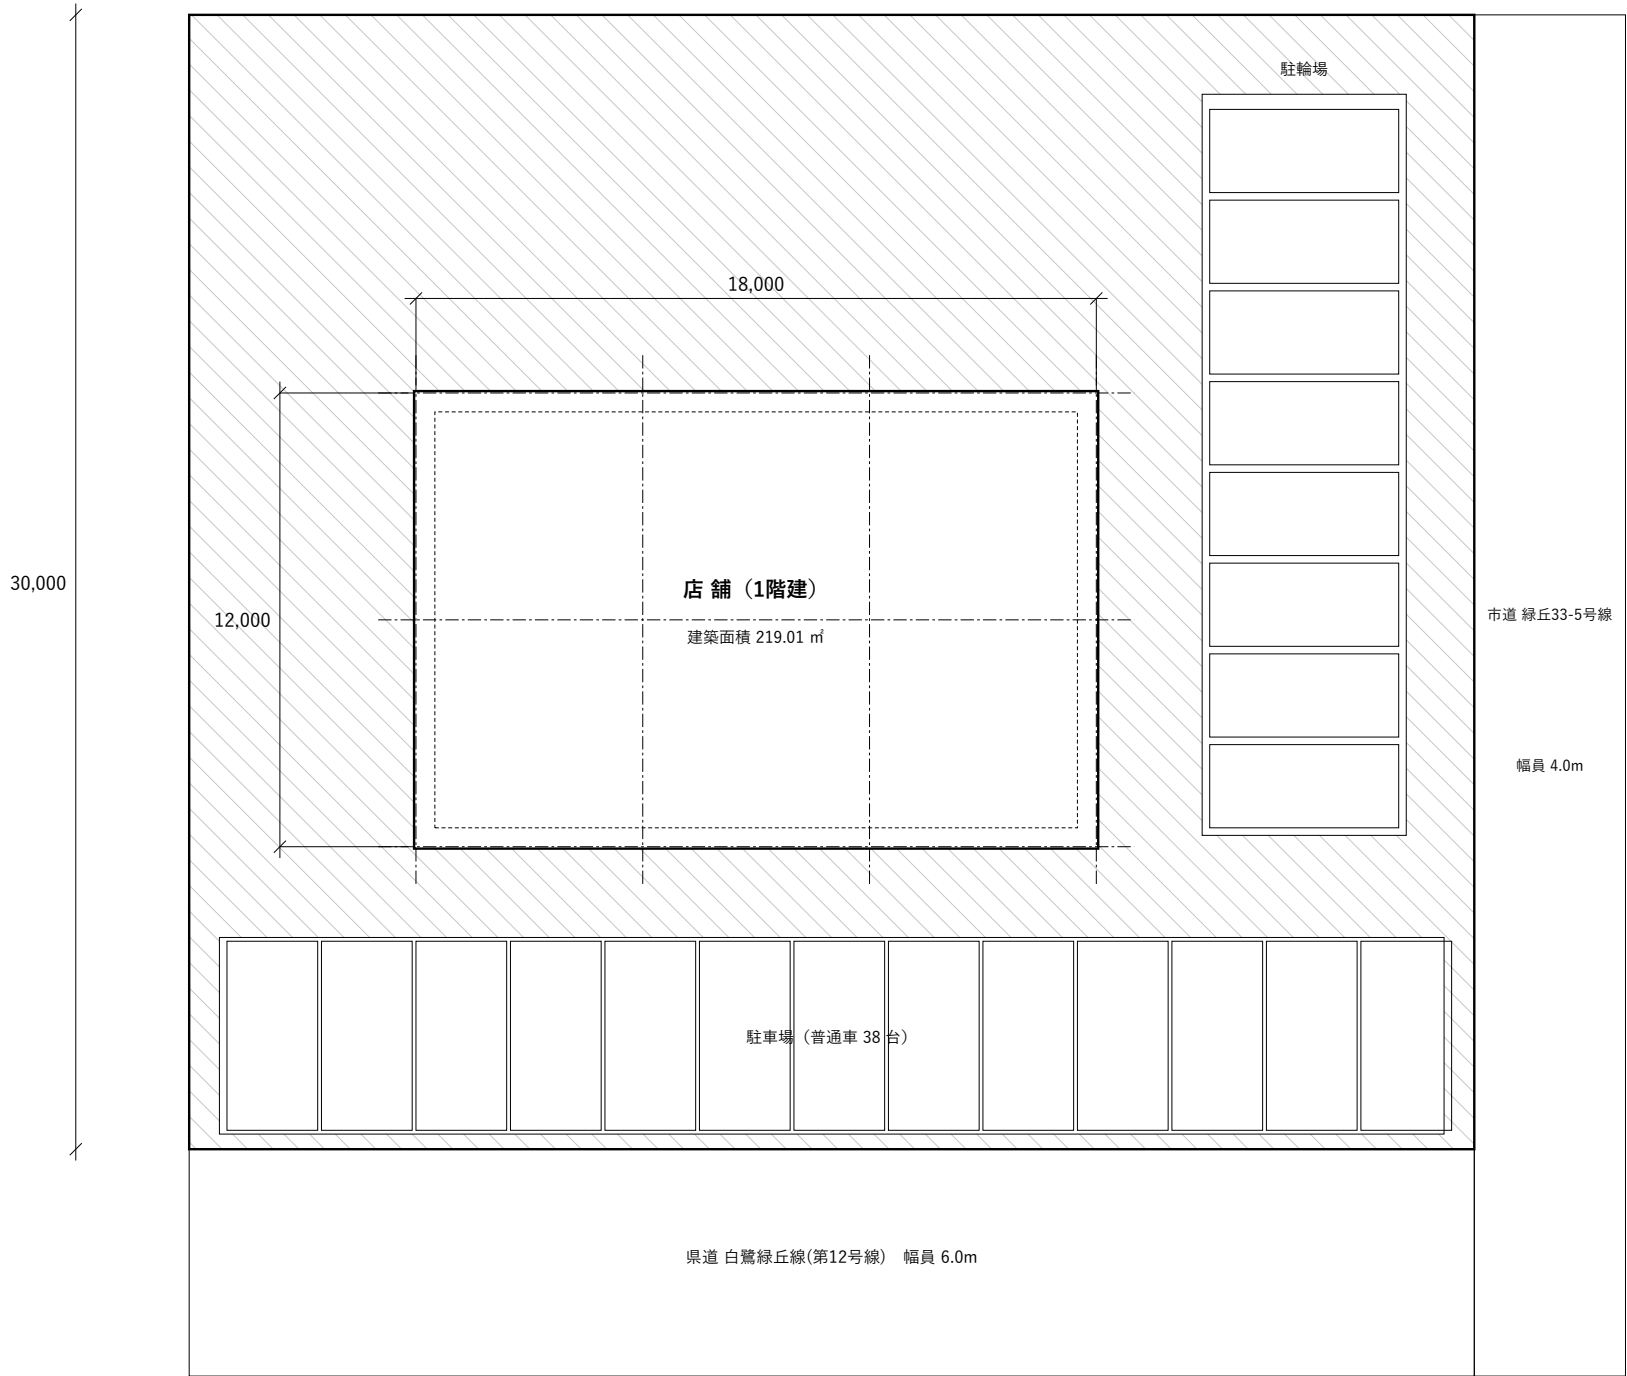

図名	配置図
所在	碧海県白鷺市緑丘三丁目14番1号
地番	碧海県白鷺市緑丘三丁目14番1、14番2
碧海県白鷺市中央三丁目1番8号	
あおば建築設計事務所	
一級建築士・管理建築士 白石 康晴	
TEL 03-0000-0000	FAX 03-0000-0001
担当 早川 真澄	

・変更略歴	 あおば建築設計事務所 一級建築士事務所 碧海県知事 登録第00013号 管理建築士 一級建築士 大臣登録 第000257号 白石 康晴		承認	検 図	作 図	受付コード： 2026-0918-014	・ T I T L E (仮称)ハルカゼストア 白鷺緑丘店 新築工事	・ N A M E 配置図		配布日
						作成日： 2026 年 9 月 18 日		・ S C A L E A1: 1/200 A3: 1/200	・ N O. A - 02	
						工事コード： HK-2026-014				

特記仕様書

工事名称	(仮称)ハルカゼストア 白鷺緑丘店 新築工事
建築場所	碧海県白鷺市緑丘三丁目14番1号
発注者	ハルカゼストア 様
設計者	あおば建築設計事務所
監理者	あおば建築設計事務所 早川 真澄

1. 一般事項

- 1-1 本仕様書は、上記工事に適用する。記載のない事項は公共建築工事標準仕様書（建築工事編）による。
- 1-2 図面と本仕様書の内容が食い違う場合は、監理者に確認のうえ指示を受ける。
- 1-3 工事に先立ち、施工計画書・施工図・見本を提出し、監理者の承認を受ける。
- 1-4 材料は原則として日本産業規格（JIS）に適合するものとする。

2. 仮設工事

- 2-1 仮囲いは高さ3.0m以上とし、出入口には扉を設ける。
- 2-2 敷地境界の確認は着工前に行き、隣地との立会い結果を書面で残す。
- 2-3 工事用電力・用水は施工者の負担とする。

3. 土工事・地業工事

- 3-1 根切り底は地盤調査報告書の支持層を確認のうえ、監理者の検査を受ける。
- 3-2 埋戻し土は良質土とし、300mmごとに転圧する。
- 3-3 捨てコンクリートは Fc18、厚さ50mmとする。

4. 鉄骨工事

- 4-1 使用鋼材は SN400B とし、ミルシートを提出する。
- 4-2 溶接は工場溶接を原則とし、全溶接部の10％以上について超音波探傷試験を行う。
- 4-3 アンカーボルトの心ずれは5mm以内とする。
- 4-4 錆止め塗装は2回塗りとし、耐火被覆部は除く。

5. 外装工事

- 5-1 ALCパネルは厚さ100mm、縦張りとし、取付金物はロッキング構法とする。
- 5-2 目地はシーリング（変成シリコーン系）とし、幅10mm・深さ8mmを標準とする。
- 5-3 屋根はガルバリウム鋼板 t=0.6 折板葺きとし、勾配は1/50とする。
- 5-4 バラベット天端はアルミ笠木とし、下端をGL+5,400とする。

6. 建具工事

- 6-1 外部アルミ建具は A-10 建具表による。耐風圧性能は 2,400Pa 以上とする。
- 6-2 自動ドアは光電式センサーとし、停電時は手動で開放できるものとする。
- 6-3 鋼製建具の板厚は t=1.6 を標準とする。

7. 内装工事

- 7-1 天井はロックウール吸音板 t=9 とし、下地は軽量鉄骨とする。
- 7-2 売場の床は塩ビ長尺シート t=2.0 とし、下地はコンクリート金ゴテ押えとする。
- 7-3 バックヤードの床は防塵塗装（エポキシ樹脂系）2回塗りとする。
- 7-4 内装制限のかかる部分は不燃材料とし、認定番号を提出する。

8. 外構工事

- 8-1 駐車場の舗装はアスファルト t=50、路盤 t=150 とする。
- 8-2 区画線は白色・幅100とし、車椅子使用者用駐車施設を1台分設ける。
- 8-3 雨水は敷地内の浸透ますで処理する。放流先は監理者の指示による。
- 8-4 植栽は在来種を用い、活着まで施工者が管理する。

9. 提出書類

- 9-1 完成時に、竣工図・保証書・取扱説明書を各2部提出する。
- 9-2 主要材料の試験成績書は、使用前に監理者へ提出する。
- 9-3 工事写真は工種ごとに撮影し、電子データで提出する。

【 質疑・確認の窓口 】

あおば建築設計事務所 担当 早川 真澄 電話番号 03-0000-0000 FAX 03-0000-0001

碧海県白鷺市中央三丁目1番8号

・変更略歴	 あおば建築設計事務所 一級建築士事務所 碧海県知事 登録第00013号 管理建築士 一級建築士 大臣登録 第000257号 白石 康晴		承認	検図	作図	受付コード： 2026-0918-014	・TITLE (仮称)ハルカゼストア 白鷺緑丘店 新築工事	・NAME 特記仕様書		配布日
						作成日： 2026 年 9 月 18 日		・SCALE A1:- A3:-	・NO. A - 03	
						工事コード： HK-2026-014				

外部仕上表

工事名称（仮称）ハルカゼストア 白鷺緑丘店 新築工事

設計 あおば建築設計事務所

建築場所 碧海県白鷺市緑丘三丁目14番1号

担当 早川 真澄

部 位	下 地	仕 上	備 考
屋 根	折板受けタイトフレーム	ガルバリウム鋼板 t=0.6 折板葺き	勾配 1/50 ・ けらば包み共
バラベツ天端	ALCパネル t=100	アルミ笠木（シルバーアルマイト）	下端 GL+5,400
外 壁（一般部）	ALCパネル t=100 縦張り	複層塗材E 吹付（アイボリー）	目地 変成シリコーン
外 壁（腰 壁）	ALCパネル t=100	複層塗材E 吹付（ダークグレー）	GL+900 まで
軒 天 井	軽量鉄骨下地	ケイ酸カルシウム板 t=6 + EP塗装	入口廻りのみ
外部建具	－	アルミ製・鋼製（A-10 建具表による）	AD-1／AW-1／AW-2／SD-1／SS-1
シャッター	－	スチール製 軽量シャッター 電動	搬入口 SS-1
外部床（歩道部）	碎石＋砂	インターロッキングブロック t=60	駐車場出入口は t=80
外部床（駐車場）	路盤 t=150	アスファルト舗装 t=50	区画線 白色 幅100
樋 ・ 排 水	－	硬質塩ビ VP75（内樋・たて樋）	排水は敷地内浸透ますへ
換気ガラリ	ALCパネル開口	アルミ製 ガラリ 600×400	北面 2箇所・FL+4,000
外部サイン	－	別途工事	位置は監理者の指示による


注1) 色は別途 色見本により監理者の承認を受ける。

注2) 本表に記載のない部位は、特記仕様書（A-03）による。


注3) 換気ガラリは建具表に含まない。符号は現場にて監理者と取り決める。

変更略歴	 あおば建築設計事務所 一級建築士事務所 碧海県知事 登録第00013号 管理建築士 一級建築士 大臣登録 第000257号 白石 康晴		承認	検 図	作 図	受付コード： 2026-0918-014	・ T I T L E (仮称)ハルカゼストア 白鷺緑丘店 新築工事	・ N A M E 外部仕上表		配布日	
						作成日： 2026 年 9 月 18 日		・ S C A L E A1:- A3:-	・ N O. A - 04		
						工事コード： HK-2026-014					

1階平面図 S=1/100

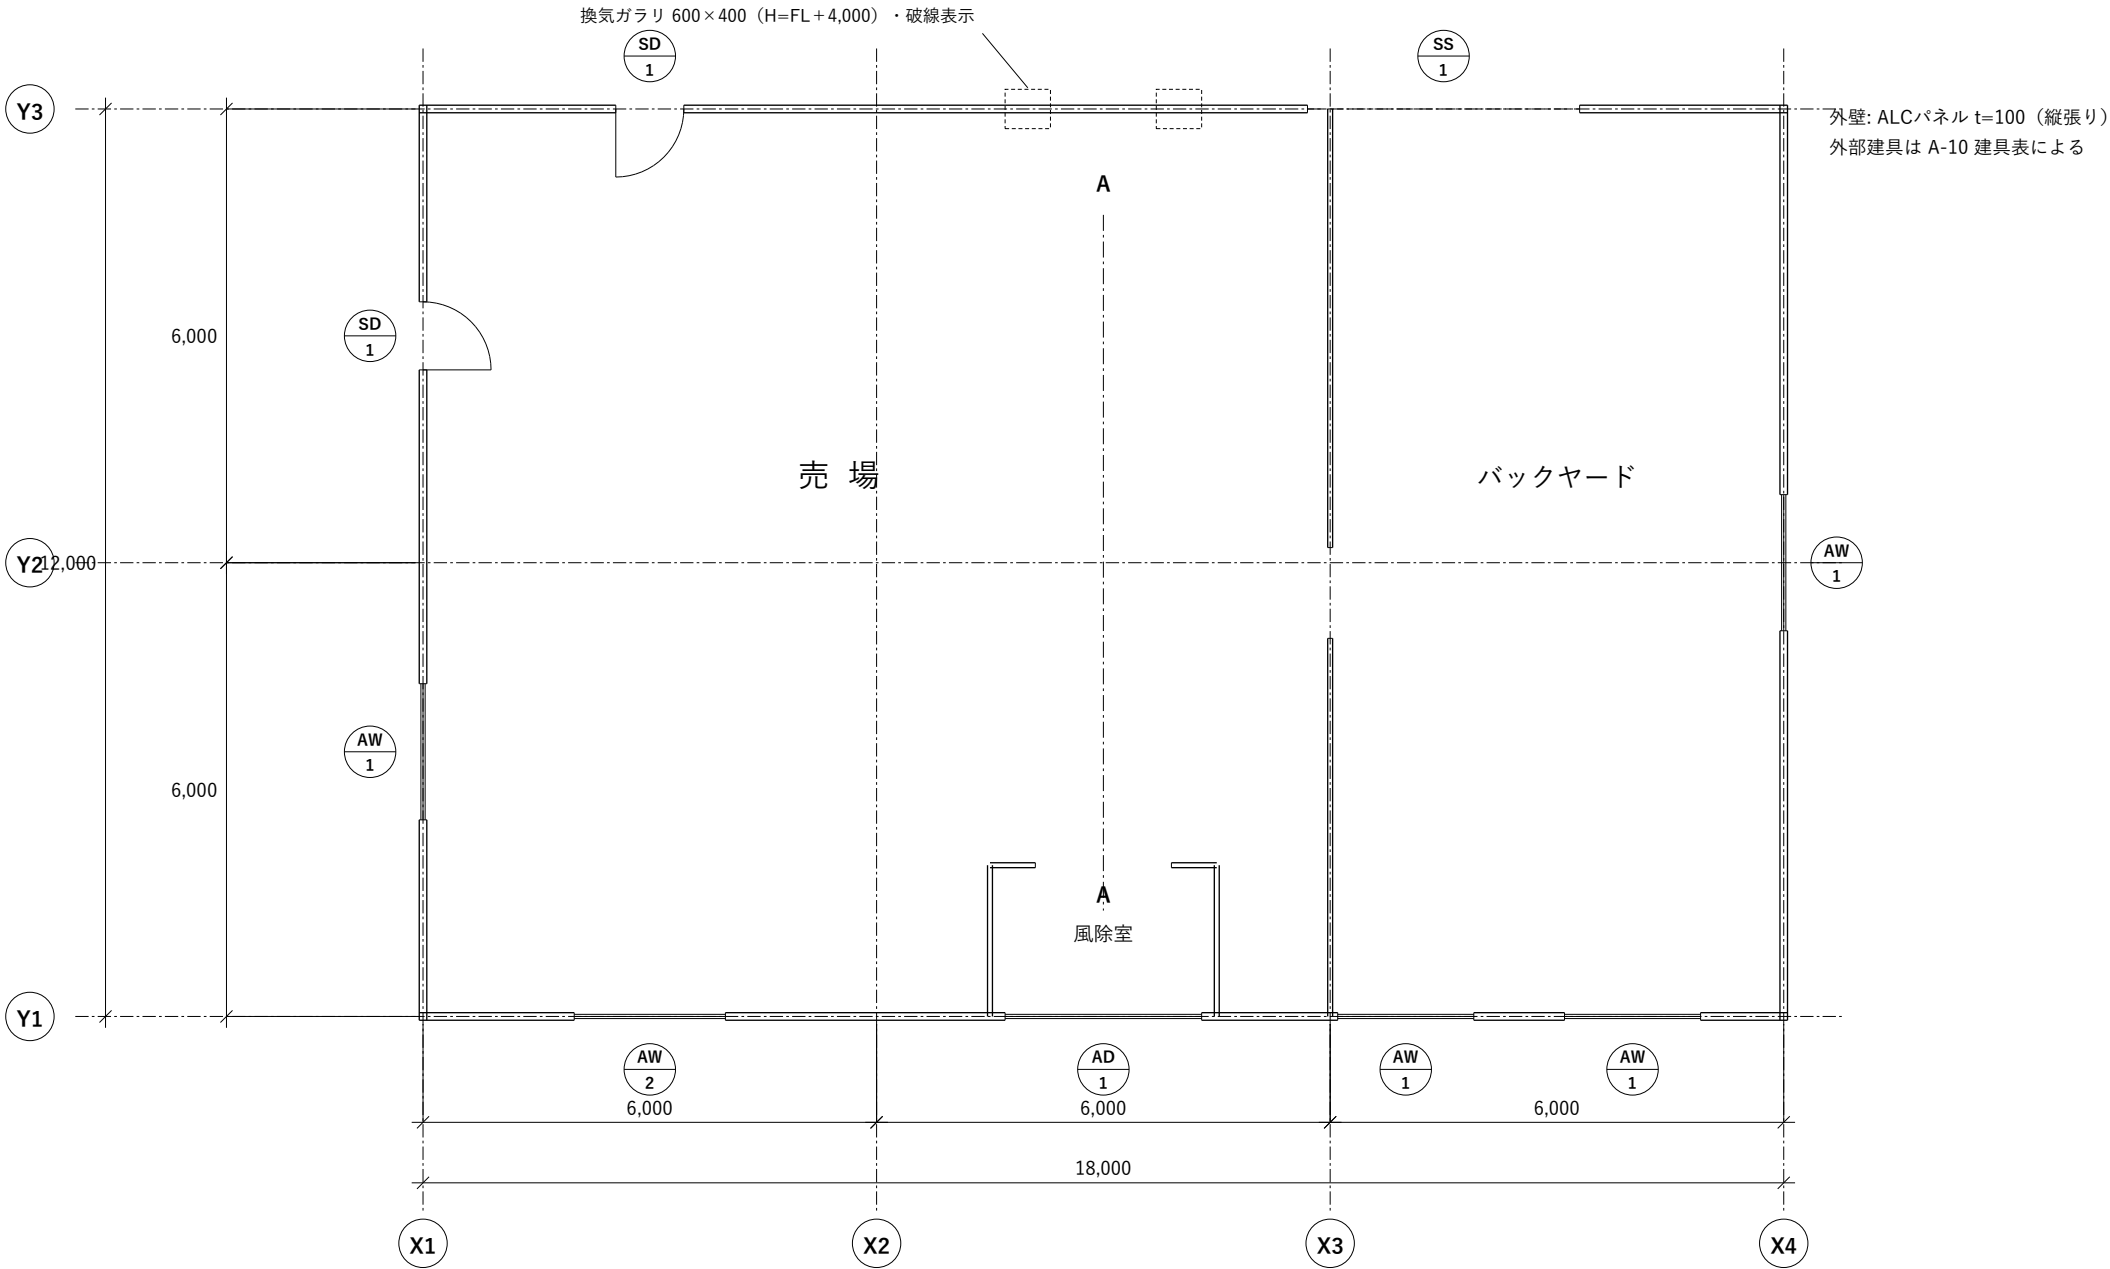


・変更略歴	 あおば建築設計事務所 一級建築士事務所 岩手県知事 登録第00013号 管理建築士 一級建築士 大臣登録 第000257号 白石 康晴		承認	検図	作図	受付コード： 2026-0918-014	・TITLE (仮称)ハルカゼストア 白鷺緑丘店 新築工事	・NAME 1階平面図		配布日
						作成日： 2026 年 9 月 18 日		・SCALE A1: 1/50 A3: 1/100	・NO. A - 05	
						工事コード： HK-2026-014				

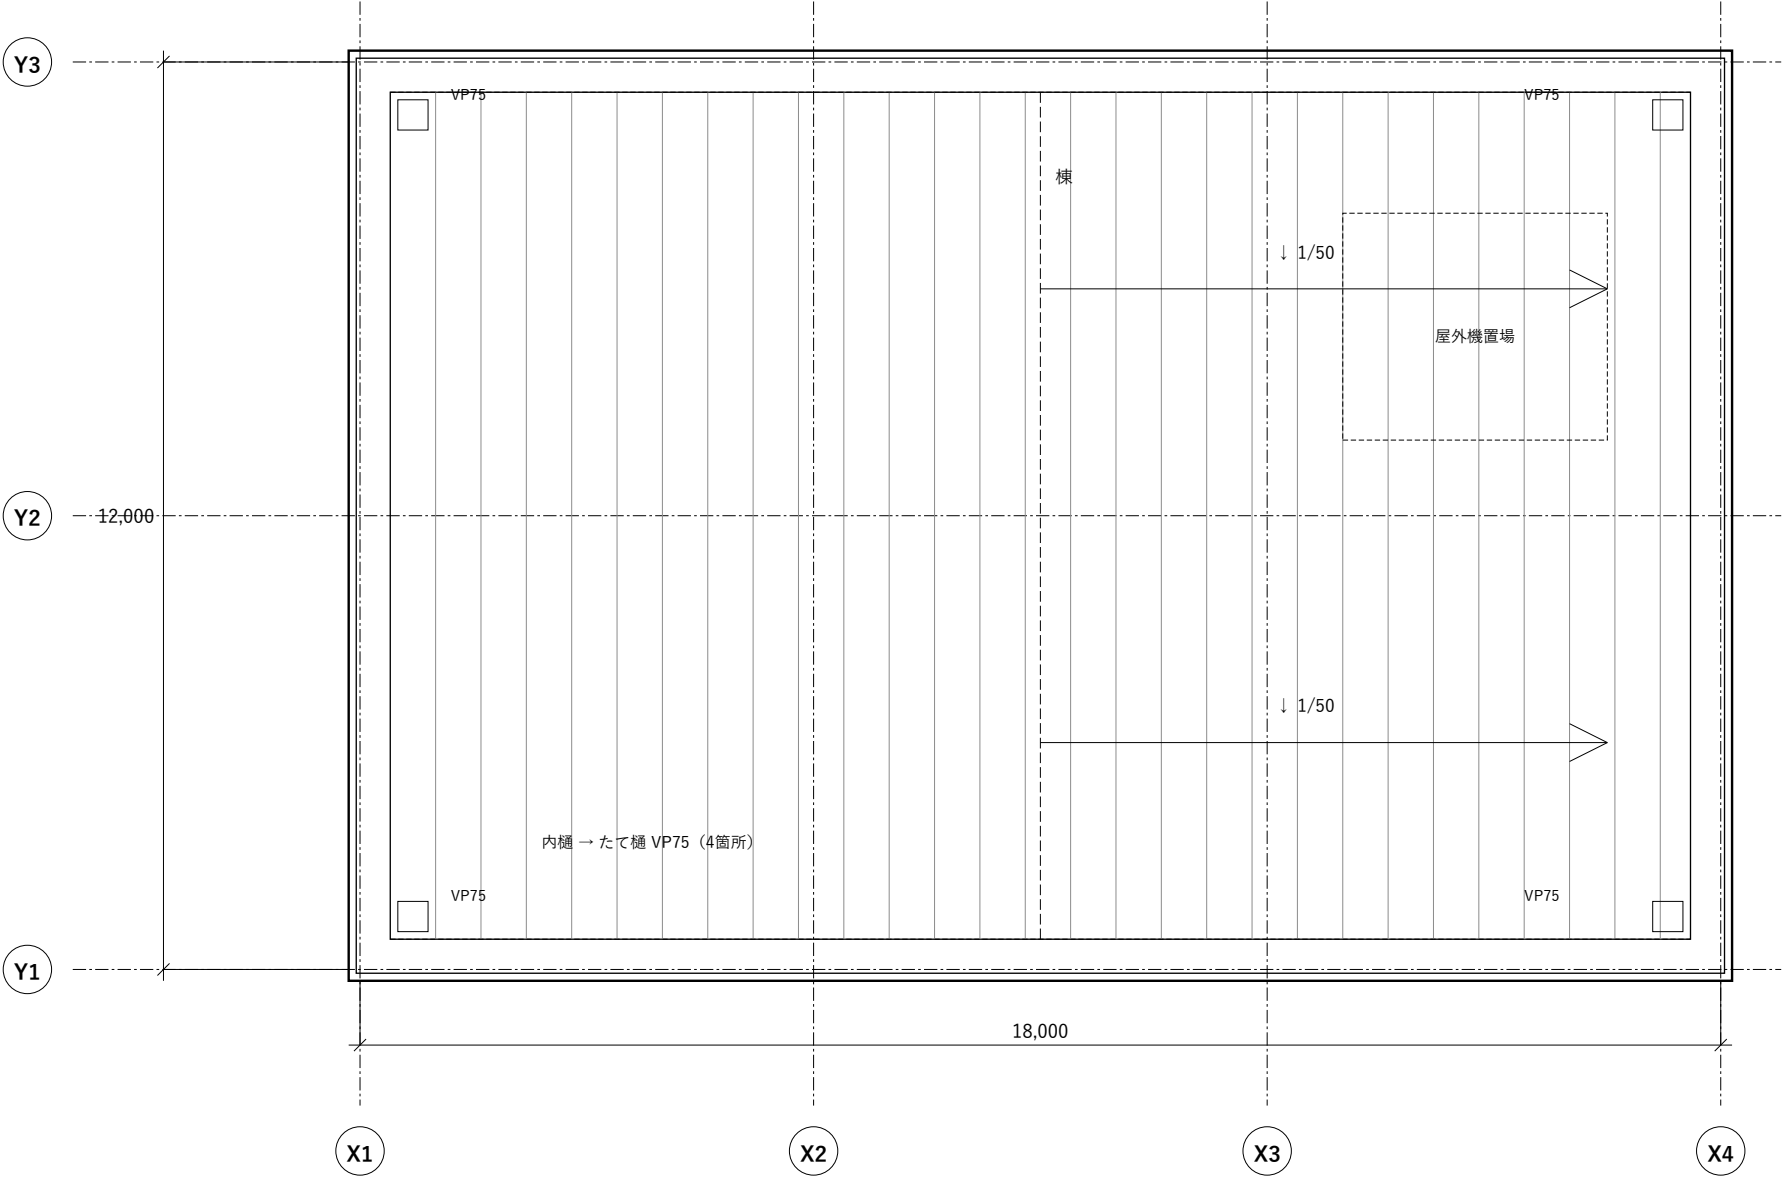


屋根: ガルバリウム鋼板 t=0.6 折板葺き (勾配 1/50)
パラベット天端 GL+5,500 / アルミ笠木 下端 GL+5,400
屋上の設備置場は別途工事とし、荷重は構造図による。




・変更略歴	 あおば建築設計事務所 一級建築士事務所 碧海県知事 登録第00013号 管理建築士 一級建築士 大臣登録 第000257号 白石 康晴		承認	検図	作図	受付コード： 2026-0918-014	・TITLE (仮称)ハルカゼストア 白鷺緑丘店 新築工事	・NAME 屋根伏図		配布日
			作成日： 2026 年 9 月 18 日	・SCALE A1: 1/50 A3: 1/100						
			工事コード： HK-2026-014	・NO. A - 06						

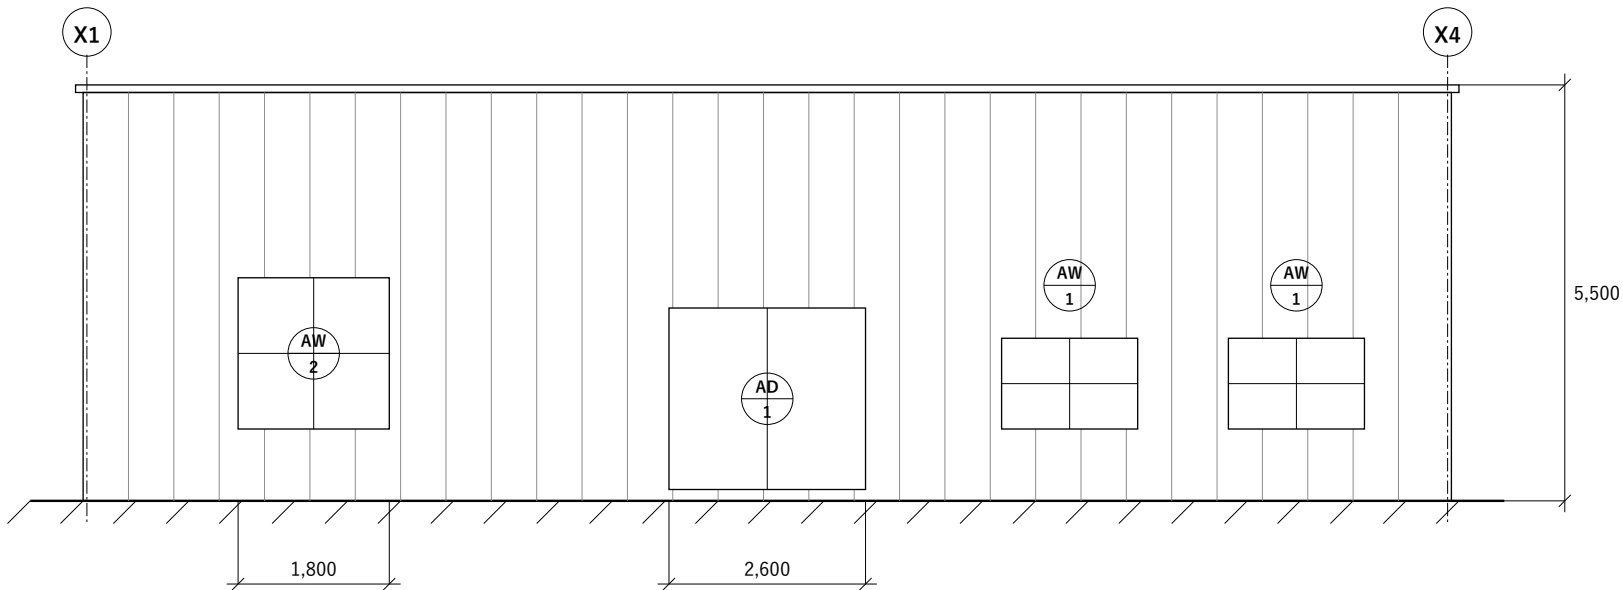


南立面図 S=1/100

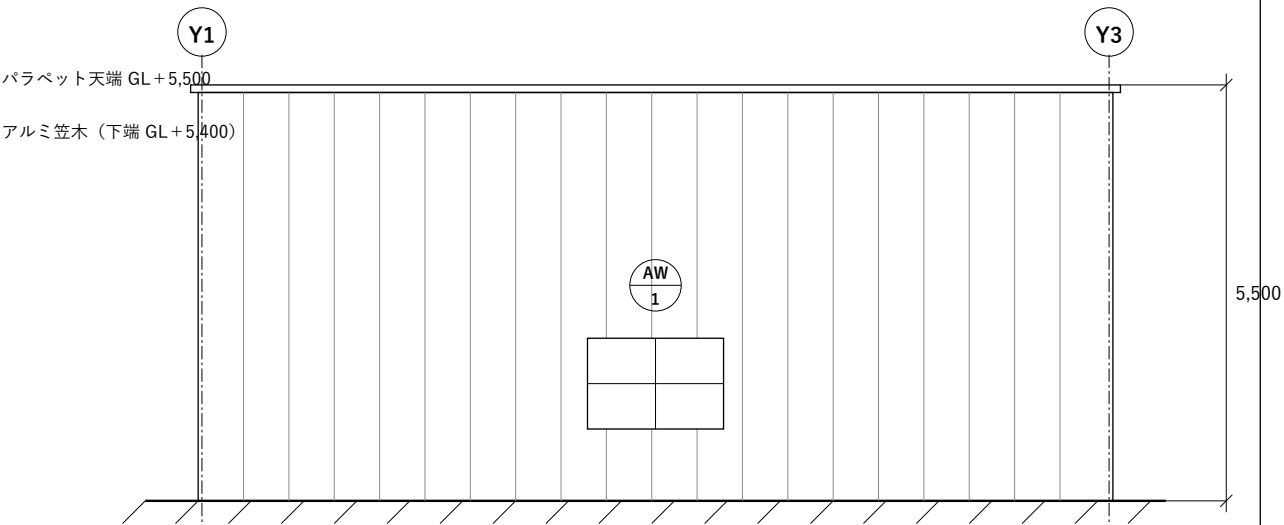

東立面図 S=1/100

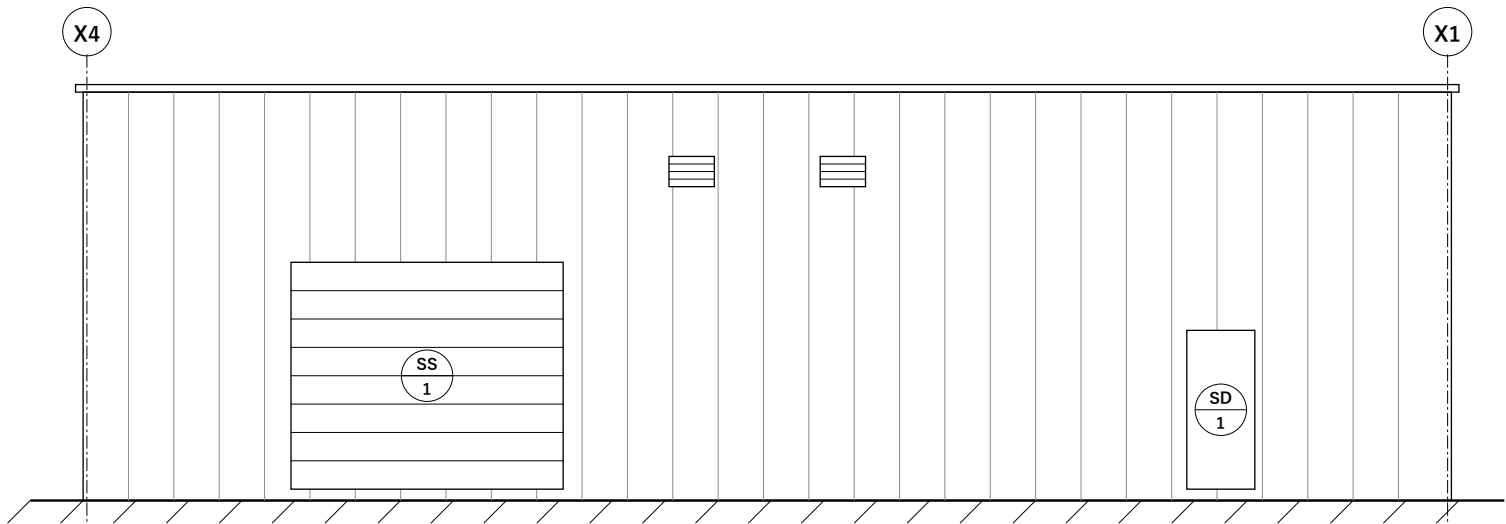

北立面図 S=1/100

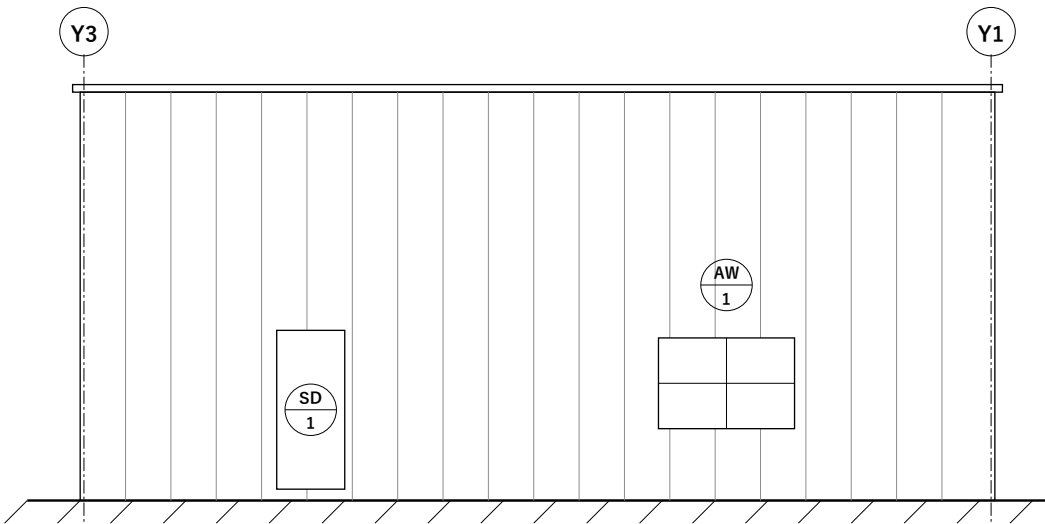


西立面図 S=1/100

外壁仕上は A-04 外部仕上表による

・変更略歴	あおば建築設計事務所 一級建築士事務所 岩手県知事 登録第00013号 管理建築士 一級建築士 大臣登録 第000257号 白石 康晴		承認	検図	作図	受付コード： 2026-0918-014	・TITLE (仮称)ハルカゼストア 白鷺緑丘店 新築工事	・NAME 立面図(東西南北)		配布日
						作成日： 2026 年 9 月 18 日		・SCALE A1: 1/50 A3: 1/100	・NO. A - 07	
						工事コード： HK-2026-014				


A - A' 断面図 S=1/100

切断位置は A-05 1階平面図による

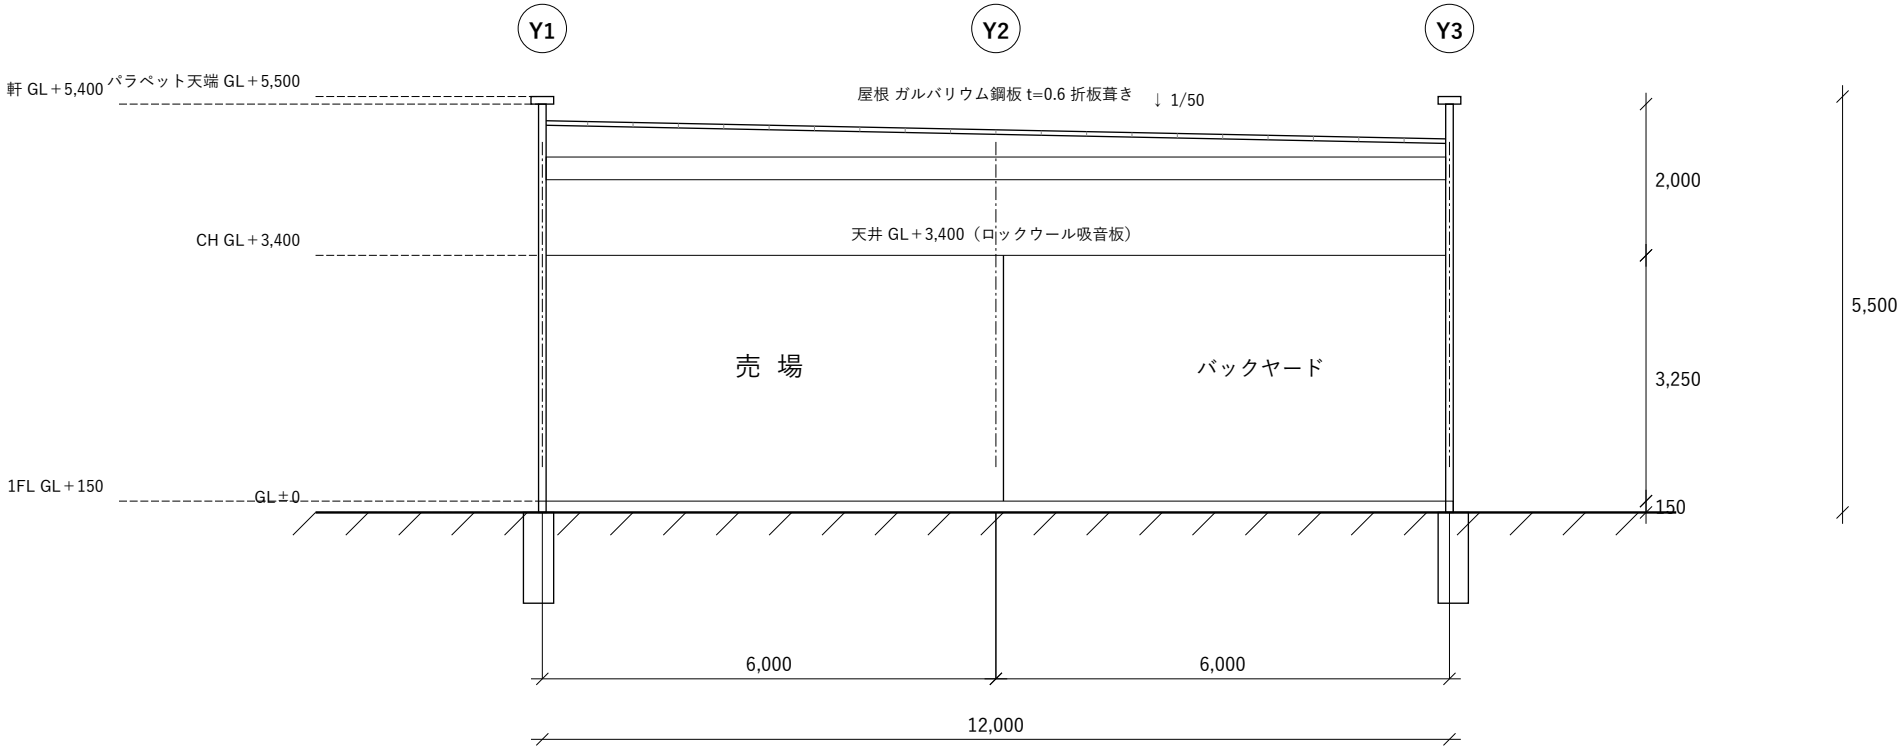

構造は鉄骨造。柱・梁の断面は構造図（別途）による。
断熱は屋根面 グラスウール t=100、外壁面 ALCパネルによる。

・変更略歴	 あおば建築設計事務所 一級建築士事務所 碧海県知事 登録第00013号 管理建築士 一級建築士 大臣登録 第000257号 白石 康晴		承認	検図	作図	受付コード： 2026-0918-014	・TITLE (仮称)ハルカゼストア 白鷺緑丘店 新築工事	・NAME 断面図		配布日
						作成日： 2026 年 9 月 18 日		・SCALE A1: 1/50 A3: 1/100		
						工事コード： HK-2026-014		・NO. A - 08		

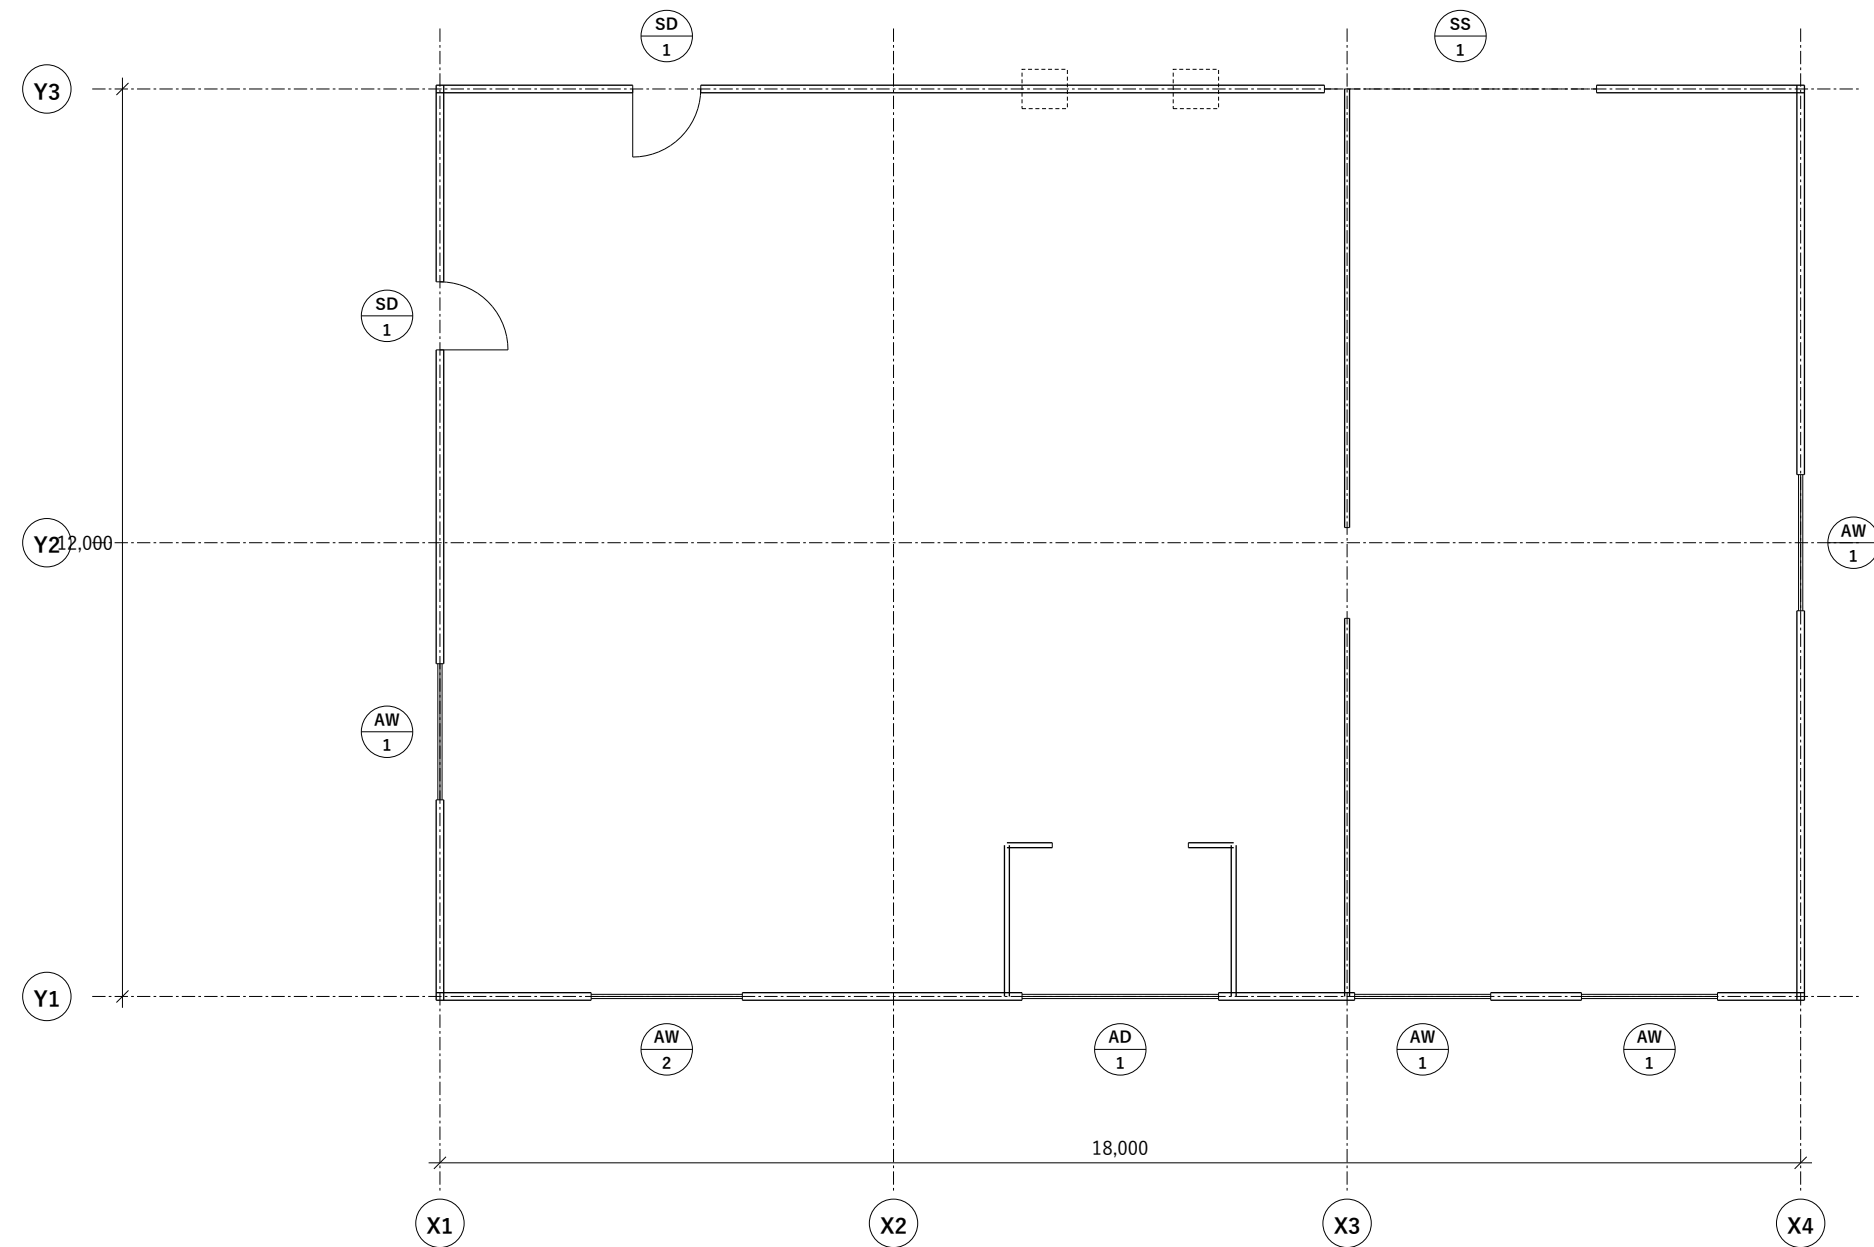

建具の位置

符号	面	位置（通り芯）	数量
AD-1	南	X芯 9,000	1
AW-2	南	X芯 3,000	1
AW-1	南	X芯 13,000	1
AW-1	南	X芯 16,000	1
SD-1	北	X芯 3,000	1
(符号なし)	北	X芯 8,000	1
(符号なし)	北	X芯 10,000	1
SS-1	北	X芯 13,500	1
AW-1	東	Y芯 6,000	1
AW-1	西	Y芯 3,500	1
SD-1	西	Y芯 9,000	1

※ 換気ガラリ（600×400）は建具表に無い。





符号は監理者（早川 真澄）の指示による。



建 具 表（外部建具）

工事名称（仮称）ハルカゼストア 白鷺緑丘店 新築工事

設計 あおば建築設計事務所 / 担当 早川 真澄

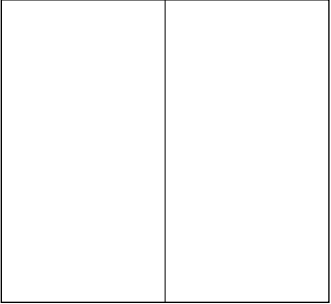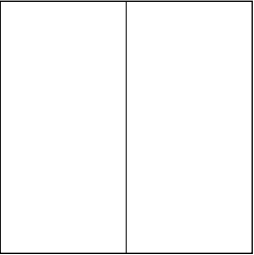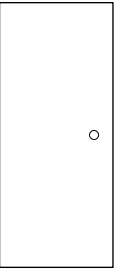 符号	AD 1	AW 1	AW 2	SD 1	SS 1
姿図	 (自動ドア(引分け))	 (引違い窓)	 (はめ殺し窓)	 (片開き扉)	 (軽量シャッター)
寸法 W×H	2,600 × 2,400	1,800 × 1,200	2,000 × 2,000	900 × 2,100	3,600 × 3,000
数量	1 箇所	4 箇所	1 箇所	2 箇所	1 箇所
材質・仕上	アルミ製	アルミ製	アルミ製	鋼製フラッシュ	スチール製・電動
ガラス	強化ガラス t=10	複層ガラス	複層ガラス	-	-
備考	正面入口・風除室	網戸付	-	錠前付	搬入口

注1) 寸法は内法基準の呼称寸法とする。取合いの詳細は施工図による。

注2) 本表は外部建具を示す。位置は A-09 建具キープランによる。

注3) 変更が生じた場合は あおば建築設計事務所（電話番号 03-0000-0000 担当 早川 真澄）まで連絡すること。

・変更略歴	 あおば建築設計事務所 一級建築士事務所 岩海県知事 登録第00013号 管理建築士 一級建築士 大臣登録 第000257号 白石 康晴		承認	検 図	作 図	受付コード： 2026-0918-014	・ T I T L E (仮称)ハルカゼストア 白鷺緑丘店 新築工事	・ N A M E 建具表		配布日	
						作成日： 2026 年 9 月 18 日		・ S C A L E A1: 1/30 A3: 1/60	・ N O. A - 10		
						工事コード： HK-2026-014					